

SECTION AT 1.7 TO PORT: EG room, crew cabin, deckhand's cabin, mess, chief engineer's cabin · looking to port · SCALE 1:50

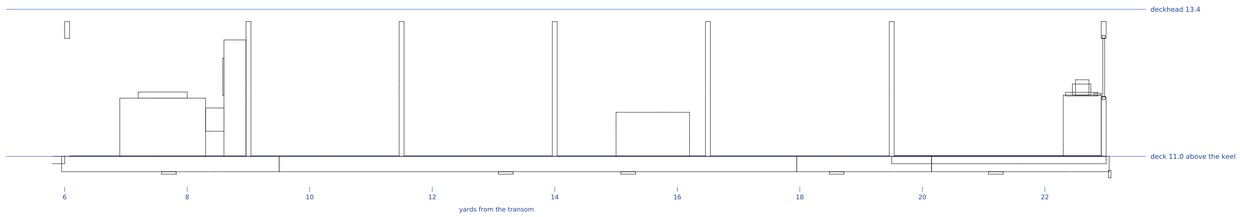


SECTION AT 1.7 TO STARBOARD: CO2 room, mate's cabin, crew WC, galley, master's cabin · looking to port · SCALE 1:50

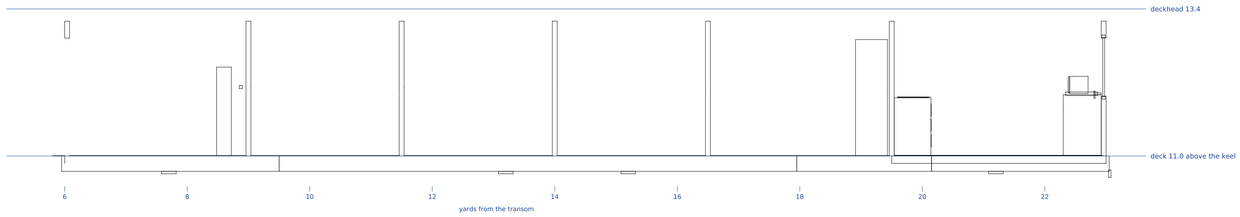

SCALE 1:50

BRIDGE DECK · PLAN · 1.0 m above the deck

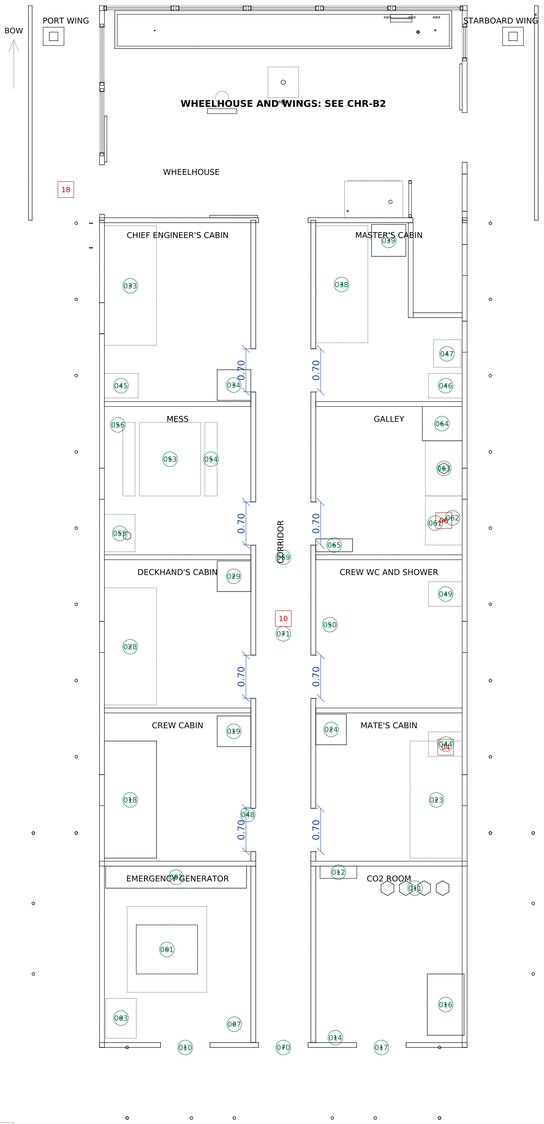

5 m

EQUIPMENT ON THE PLAN (register B001–B116; tag = the Town's KKS where it gave one)

001 Emergency generator, 40 kVA / 32 kW · 15MKA10 AG001
002 Emergency switchboard (ESB), 440 V and 1 · 10BRV10 GS001
003 24 V battery bank (starting and radio/em · 10BTA10 GS001
007 Day tank, 60 L
010 Exit door to the open deck (weathertight
011 CO_2 bottles, 4 × 45 kg · 10SGJ10 BB001
012 CO_2 release cabinet · 10SGJ10 CH001
014 Remote fan stops
016 Firemen's outfit locker, two outfits
017 Exit door to the open deck
018 Bunk (two berths, stacked)
019 Locker
023 Bunk (one berth)
024 Locker
028 Bunk (one berth)
029 Locker
033 Bunk (one berth)
034 Locker
038 Bunk (one berth)
039 Locker
044 Desk
045 Desk
046 Desk
047 Safe (ship's papers)
048 Duty-berth name plate (relief engineer)
049 WC · 10GHB10 BR001 (shared)
050 Basin · 10GKB20 BR002 (shared)
053 Mess table (for six)
054 Mess benches (two)
055 Sideboard
056 Television
061 Three-plate range, 6 kW · 10GKB30 AH001
062 Hood and extract
063 Sink · 10GKB20 BR001
064 Fridge-freezer · 10GKB30 GS001 (shared)
065 Provision locker
069 Ceiling lights (five) · 10BRV20 GS011
070 Red plate over the aft crew door (an exi
071 Handrails along the corridor

FINDINGS WITH A PLACE ON THIS PLAN (CHR-B5 has all)

BF-04 [error] The Town's own audit still lists 8 findings on this deck
BF-06 [error] The galley range is tagged as drinking water
BF-10 [risk] The cabin doors are 0.70 m wide; every other door on the deck is 0.80 m
BF-18 [risk] One hydrant and a 15 m hose do not reach the aft half of the bridge deck

Drawn from ferry/data/ferry.bin.gz and the Town data at the commit below; not for construction
THE CHRISTINA · bridge survey, Rev A

BRIDGE DECK · general arrangement

Plan cut 1.0 m above the deck, with equipment tags and findings
Scale 1:50 plan and sections
Metres on the sheet at the stated scale; DXF in sheet millimetres
ferry.bin.gz · Town f0b2973

Drawing no.
CHR-B1