SK-ZF-001 Floor finishes - every floor laid flush or at least 10 mm clear of the next

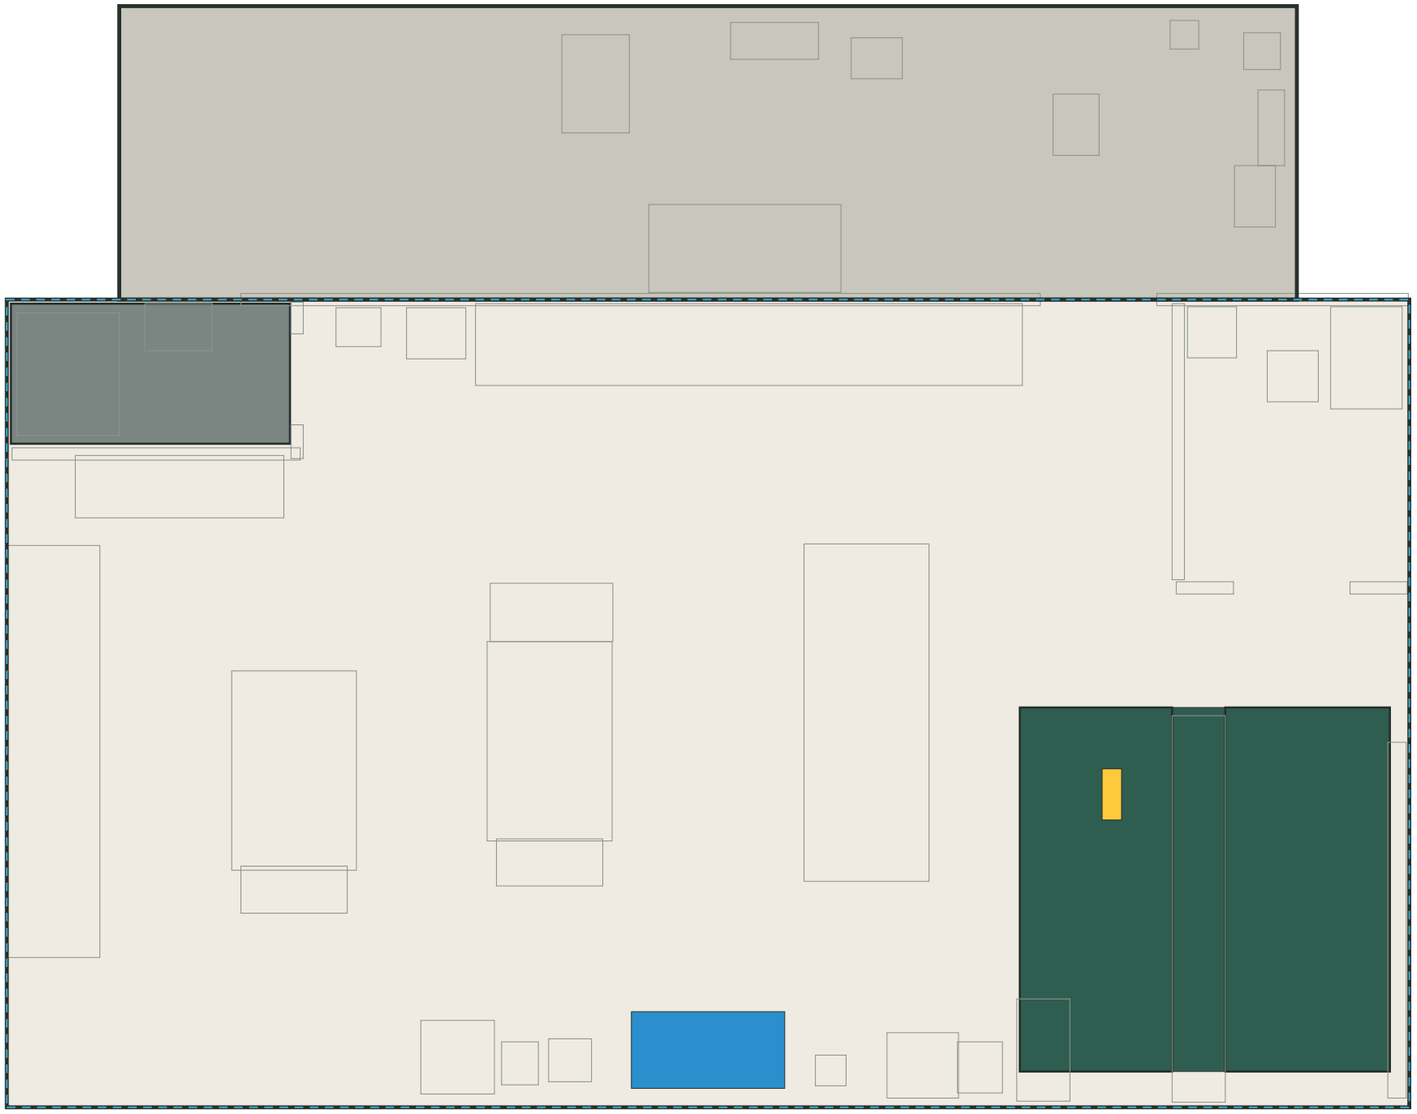

- Terrazzo ±0 (cut round the insets) [solid]
- Back-room screed +1 [solid]
- Till tiles ±0, flush in the terrazzo [solid]
- Restroom mosaic ±0, flush [solid]
- Sheen glaze +4, no depth write, cut round the insets [glaze (no depth)]
- Welcome mat +10, decal [decal (offset -2/-4)]
- Till sticker +7, decal [decal (offset -2/-4)]
- Paw stickers +7, glaze [glaze (no depth)]

Rules for what lies on the floor (SK-ZF-002):
- an inset (till tiles, restroom mosaic) is laid in the floor: the terrazzo and its sheen are cut round it, the two meet edge to edge at the same level;
- a covering on the floor is a decal (polygon offset) at least 7 mm up, or a glaze that writes no depth (the sheen, the paw stickers);
- nothing solid lies within 10 mm of another floor over more than 0.01 m2.

Was: the till tiles laid 6 mm over the terrazzo, over 11 m2 (SK-ZF-003); the restroom mosaic a decal 3 mm over it; the mat and rug inside the sheen.

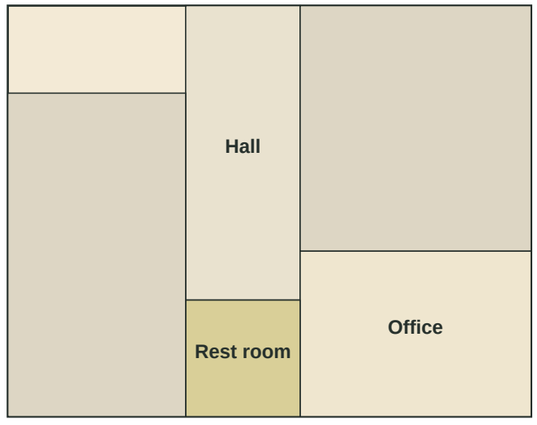

Upper floor (kept): office 5.65 x 4.05 m, rest room 4.5 mats, hall, stores

SK-ZF-001 rev A 26 October 2026

Sakura Shoten, Minato - surfaces as built in Johansson World

Floor finishes, ground floor 1:60; upper floor key plan 1:150

Virtual-environment drawing, not a construction approval.

SK-ZF-002 Every course starts where the last ends; a print is a decal on what it is printed on

1. Two faces that look the same way never lie within 2 mm of one plane where they overlap (tests/sakura-surfaces.test.mjs).
2. Joinery is built in courses that butt: a board ends at the panel it meets, a rail stands at least 3 mm proud of the board edge it fronts, a post 5 mm proud of the panel behind it. No box runs through another with its faces in the other's plane.
3. Printed paper, labels, screens and stickers are decals: drawn with polygon offset (factor -1, units -4) on what they are printed on. Two decals with the same offset never share a plane (the scanner compares them too: offsetPairs).
4. Floors: an inset is cut into the floor it sits in; a covering is a decal or a glaze; solid layers keep 10 mm apart.
5. Packs on the shelves are built the same way: a can's body runs between its beads, a lid sits inside its rim flange, a crust is a ring round its crumb, clear film has no underside on the shelf.
6. Nothing passes through a wall: each ceiling tube ends within its run (two hung through the partition and the office wall).

A Can (beer, coffee, tuna, peaches) 1:1

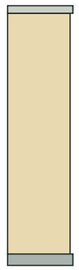

- body 6..133
- base bead 0..6
- lid bead 133..137

Was: body 0..135 with both beads round it,
1.5 mm off its faces. Now the body runs between them.

B Ramen cup lid 4:1

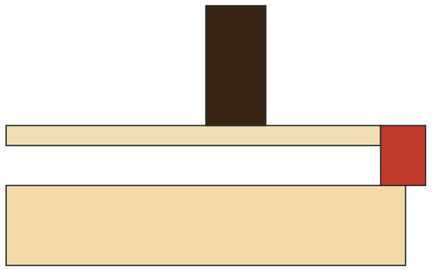

- cup to 128
- foil, flush with flange at 131
- rim flange 128..131
- tab, 3 mm up

Was: foil 0.25 mm under the rim top, overlapping it.
Now the foil sits inside the flange ring.

C Gondola board and price rail 2:1

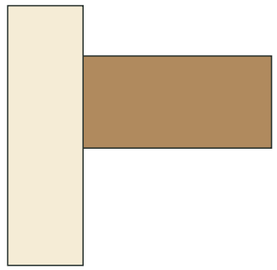

- board, level-22..level
- price rail, 3 mm proud

Was: rail flush with the board's edge.
Now 3 mm proud, the edge inside it.

D Wainscot 1:5

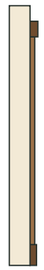

- skirting 0..80
- wood 80..880
- rail 880..940
- plaster

Was: wood to 900, under the rail from 880.
Now each course starts where the last ends.

E Shopfront posts, plan 1:5

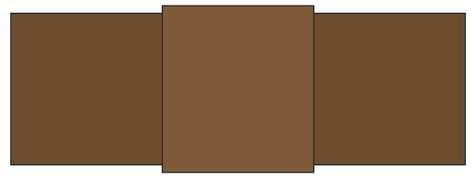

- kick panel F-40..F+60
- post, 5 mm proud both faces

Was: posts and panels in one plane.
Now posts stand 5 mm proud; door posts 5 mm proud of the transom.

F Till tiles in the terrazzo, section 1:2

- terrazzo ±0
- till tiles ±0, the terrazzo cut round them
- sheen glaze +4 (cut round the tiles)

Was: tiles laid 6 mm over the terrazzo and its sheen.

G Cooler carcass, plan 1:10

- back panel
- side, in front of the back
- plinth / head between the sides

Was: plinth, head and sides overlapping the back,
their ends in its plane.

SK-ZF-002 rev A 26 October 2026

Sakura Shoten, Minato - surfaces as built in Johansson World

Surface rules and typical joints, as rebuilt

Virtual-environment drawing, not a construction approval.

SK-ZF-003 Faces in one plane, before (circles, sized by area) and after (none)

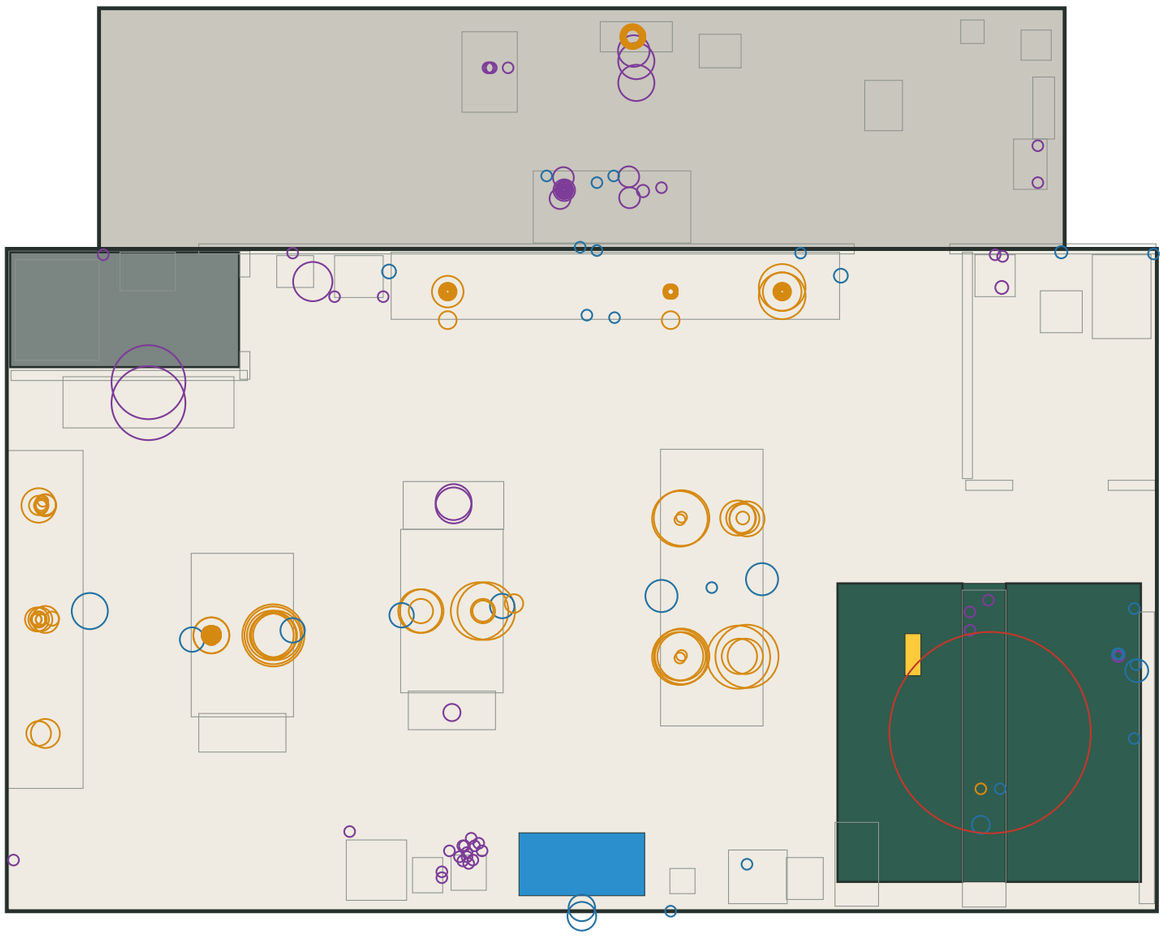

Both storeys	before: pairs / m2	after
Floors	1 / 11.04	0 / 0.00
Products	143 / 24.35	0 / 0.00
Joinery	34 / 2.74	0 / 0.00
Prints and props	64 / 6.16	0 / 0.00
Total	**242 / 44.29**	**0 / 0.00**

Scanner: tools/z-fighting.mjs, 2 mm and 4 cm2 (floors: 10 mm and 0.01 m2), decals compared with each other, faces hidden inside a closed solid left out.
Before: tools/sakura-surface-audit.mjs on main a098bbe5 (audit-before.json).
After: the same tool on this revision (audit.json).

Checks:

pass shop: no two faces within 2 mm of one plane
pass shop: no floor layer within 10 mm of another
pass office: no two faces within 2 mm of one plane
pass office: no floor layer within 10 mm of another
pass sakura-floor at floor level
pass Sakura till floor at floor level
pass Restroom mosaic floor at floor level
pass the sheen is a glaze (writes no depth)
pass Sakura welcome mat is a decal
pass Sakura till sticker is a decal
pass DXF reopens with no audit errors

SK-ZF-003 rev A 26 October 2026

Sakura Shoten, Minato - surfaces as built in Johansson World

Surface audit: main a098bbe5 against revision A

Virtual-environment drawing, not a construction approval.