
STARBOARD PROFILE


SCALE 1:100

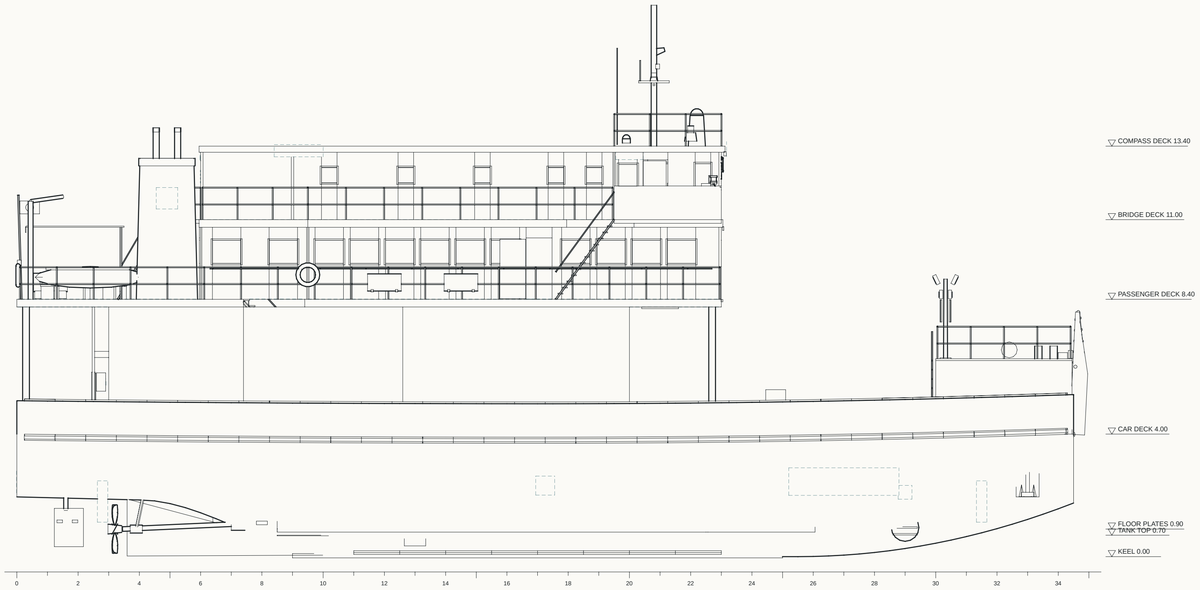

yard: metres from the transom


BOW, LOOKING AFT

SCALE 1:100

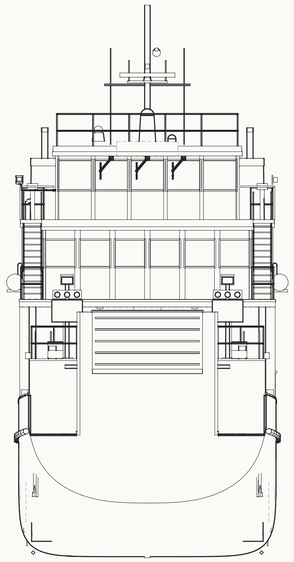

STERN, LOOKING FWD

SCALE 1:100

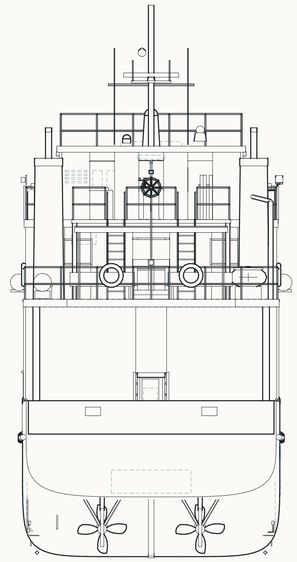

ISSUES IN THIS SECTION · 0 clash, 1 check

30 Navigation feeder fallback › Navigation panel, protection and actual two-core cable, two of its faces, share a plane over 15 cm²: they flash
WING S · yard 22.75 · x 4.18 S · h 12.15

PORT PROFILE

SCALE 1:100

BODY SECTION AT 3.0

SCALE 1:100

BODY SECTION AT 11.0

SCALE 1:100

BODY SECTION AT 20.5

SCALE 1:100

PLAN FROM ABOVE

SCALE 1:100

yard: metres from the transom

BODY SECTION AT 31.0

SCALE 1:100

NOTES

Drawn from buildFerryModel() as the game builds it: plans are cut by a horizontal plane and sections by a vertical one, and what is cut is drawn heavy, what lies beyond in outline. The design (general arrangement, ferry-ship.js) is dashed over each plan: a room built away from its design shows.


Issues are found in her data by tools/ferry-audit.mjs and numbered for the whole set: red a clash, amber a check. Their source lines are in issues.json.

YARD Johansson Shipyard, Innoshima **JOHANSSON SHIPYARD**	SHIP M/V MINATO MARU hull No. 127, built 1994		DRAWING No. **JS-127-C1**
TITLE EXTERIOR · at sea, ramp raised **Profiles, plan, bow and stern elevations and four body sections**			SCALE 1:100 on A1
SOURCE tools/ferry-cad.mjs	DATA buildFerryModel() as built	STATUS WORKING DRAWING	SHEET 1 / 8
DRAWN Claude, AI survey	CHECKED owner review open	DATE 2026-11-09	REV C · working set by section

WORKING DRAWINGS OF THE GAME MODEL · Johansson World vessel · no flag, class or construction approval · buildFerryModel() as built, cut and drawn with hidden lines removed · issues from tools/ferry-audit.mjs

CAR DECK · plan cut 1.5 m above it

SCALE 1:50

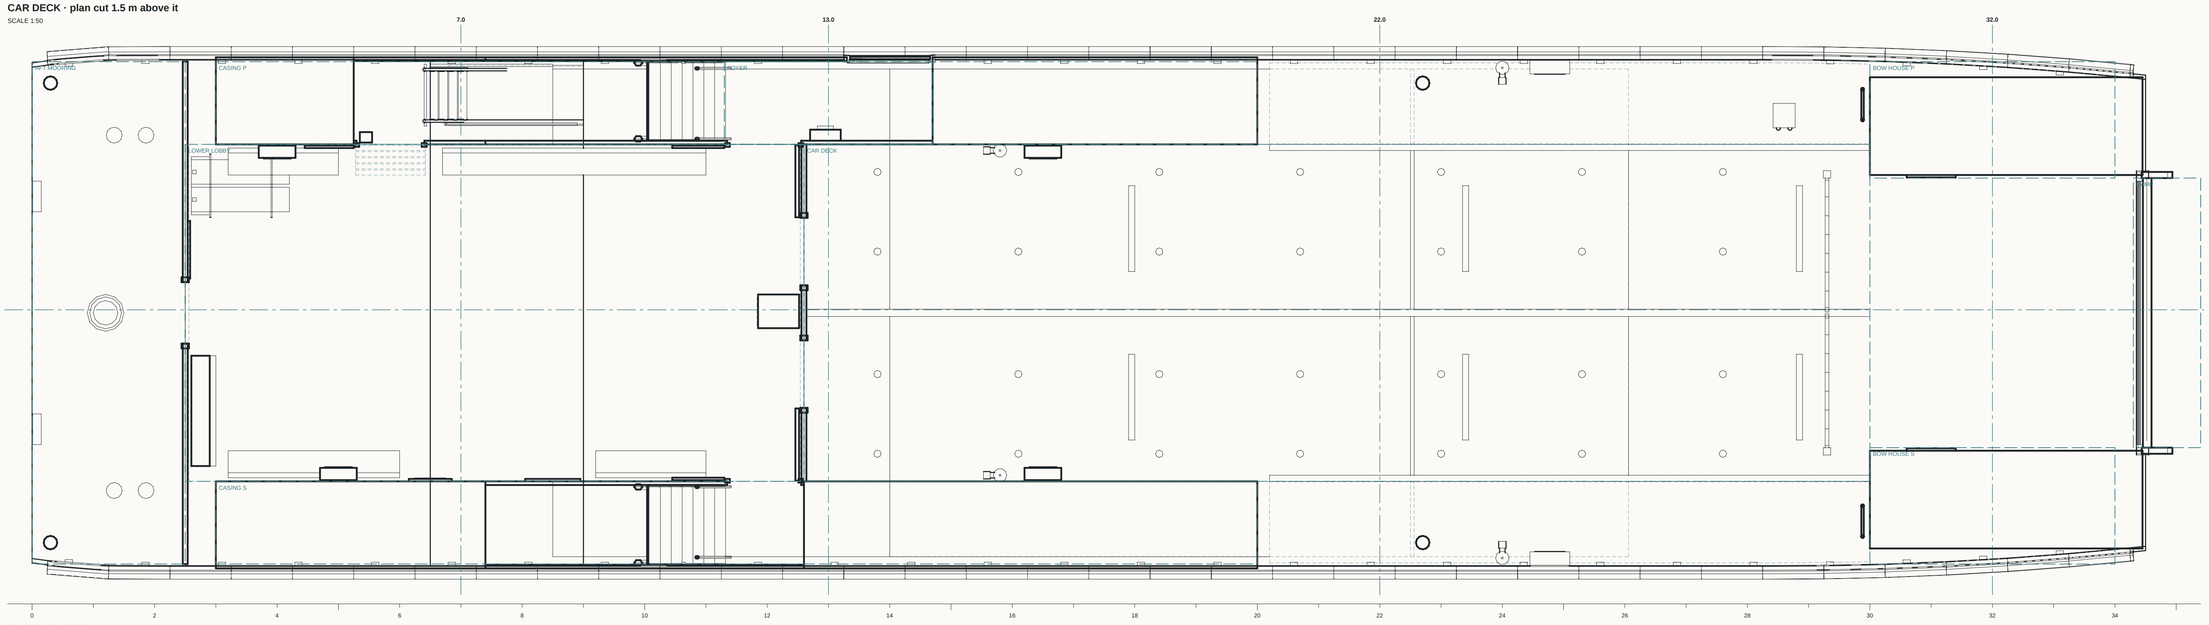

yard: metres from the transom

LINES AND MARKS

- Cut by the plane
- Outline beyond
- Feature edges
- The design (general arrangement)
- Where a section is taken
- 1 Clash: wrong, to fix
- 2 Check: look at it

SECTION ON THE CENTRELINE · looking to port

SCALE 1:50

yard: metres from the transom

AT 7.0 · LOWER LOBBY

SCALE 1:50

AT 13.0 · FOYER AND CASINGS

SCALE 1:50

AT 22.0 · LANES

SCALE 1:50

AT 32.0 · BOW HOUSES

SCALE 1:50

ISSUES IN THIS SECTION · 0 clash, 0 check

None found by the audit. What it cannot see (a door in the wrong place, a missing handrail, a room wrong for its use) is for the owner's review of the drawing.

NOTES


Drawn from buildFerryModel() as the game builds it: plans are cut by a horizontal plane and sections by a vertical one, and what is cut is drawn heavy, what lies beyond in outline. The design (general arrangement, ferry-ship.js) is dashed over each plan: a room built away from its design shows.

Issues are found in her data by tools/ferry-audit.mjs and numbered for the whole set: red a clash, amber a check. Their source lines are in issues.json.

YARD Johansson Shipyard, Innoshima **JOHANSSON SHIPYARD**	SHIP M/V MINATO MARU hull No. 127, built 1994		DRAWING No. **JS-127-C2**
TITLE CAR DECK **Lanes, casings, lower lobby, foyer, bow houses and mooring stations**			SCALE 1:50 on A1
SOURCE tools/ferry-cad.mjs	DATA buildFerryModel() as built	STATUS WORKING DRAWING	SHEET 2 / 8
DRAWN Claude, AI survey	CHECKED owner review open	DATE 2026-11-09	REV C - working set by section

MACHINERY SPACES · plan cut 1.5 m above the floor plates

SCALE 1:50

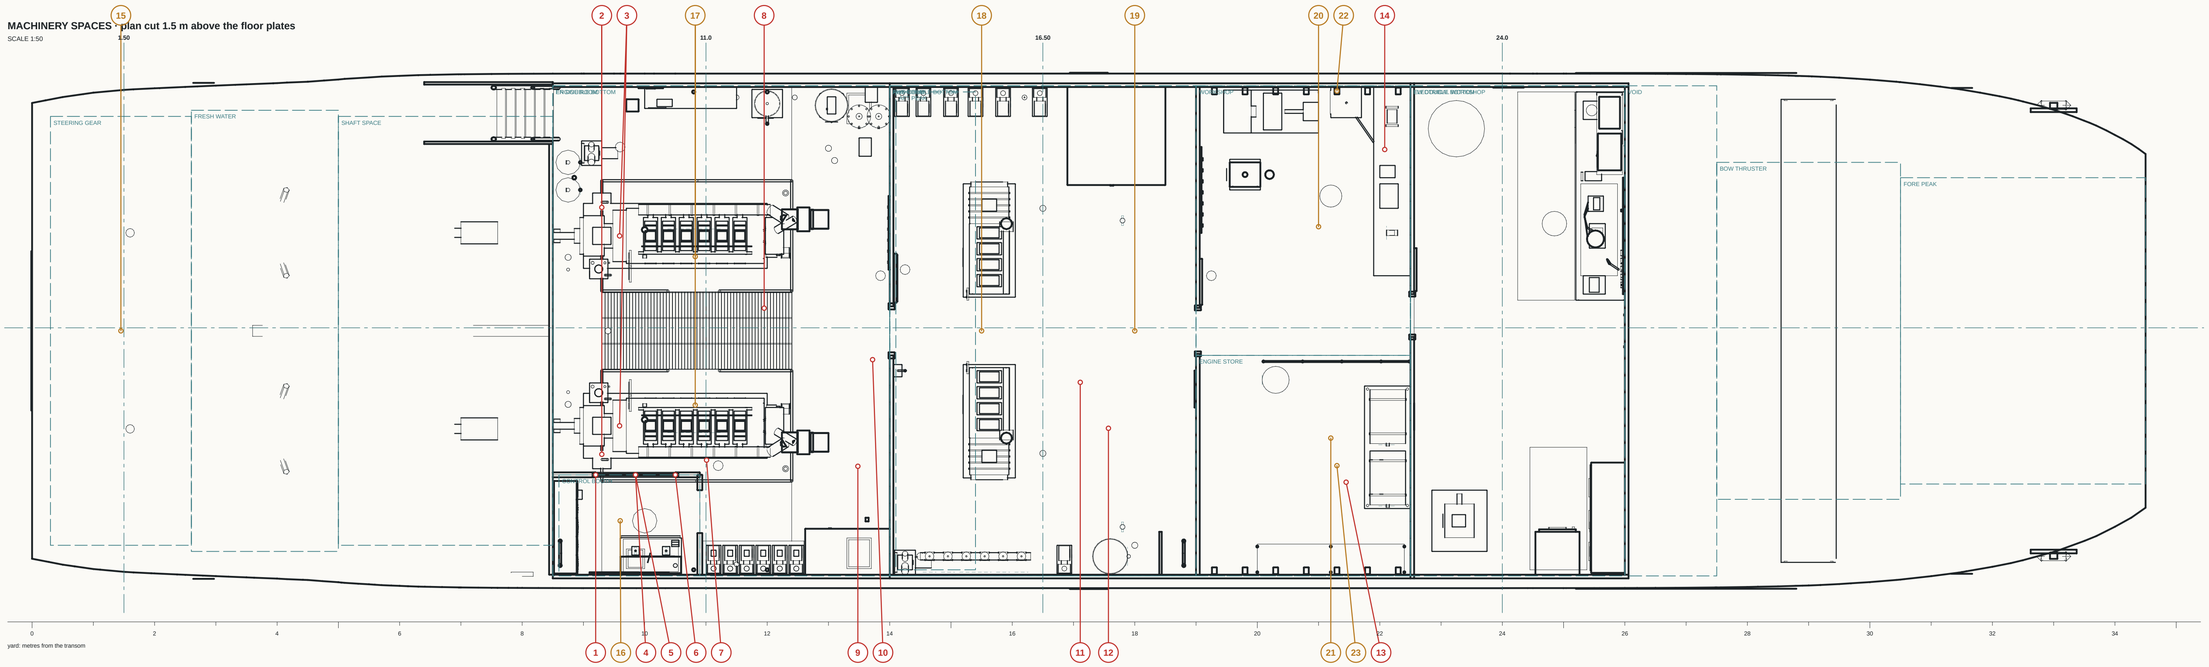

yard: metres from the transom


SECTION ON THE CENTRELINE · looking to port

SCALE 1:50

yard: metres from the transom


AT 1.5 · STEERING GEAR

SCALE 1:50

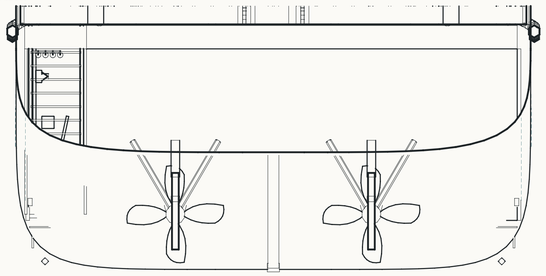


AT 11.0 · ENGINE ROOM

SCALE 1:50

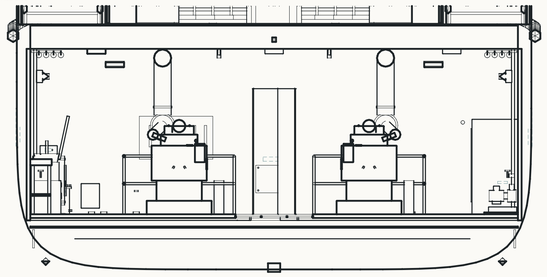


AT 16.5 · AUXILIARY ROOM

SCALE 1:50

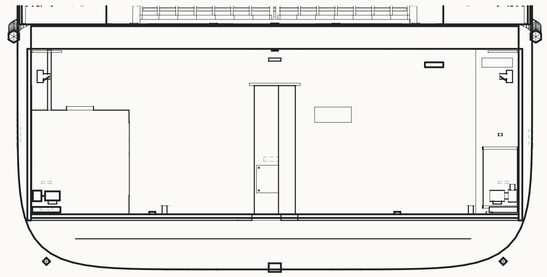

AT 24.0 · ELECTRICAL WORKSHOP

SCALE 1:50

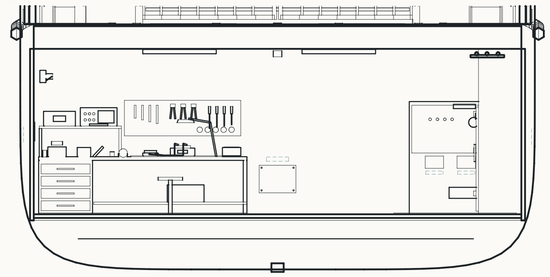

LINES AND MARKS

- Cut by the plane
- Outline beyond
- Feature edges
- The design (general arrangement)
- Where a section is taken
- (1) Clash: wrong, to fix
- (2) Check: look at it

ISSUES IN THIS SECTION · 14 clash, 9 check

1. the engine room's Blender model (Cube509) and her metal work share a plane over 400 cm²: they flash
   CONTROL BOOTH · yard 9.20 · x 2.35 S · h 2.25 · ferry-model.js:604
2. main engine bedplate and local control stand occupy the same space, 13 cm deep (in the code-built engine room, seen until the Blender model loads)
   ENGINE ROOM · yard 9.38 · x ±2.02 · h 1.01 · ferry-interior.js:815, ferry-interior.js:1056
3. main engine bedplate and flywheel housing occupy the same space, 4 cm deep (in the code-built engine room, seen until the Blender model loads)
   ENGINE ROOM · yard 9.59 · x ±1.55 · h 1.10 · ferry-interior.js:815
4. the engine room's Blender model (Cube509) and her metal work share a plane over 644 cm²: they flash
   CONTROL BOOTH · yard 9.85 · x 2.35 S · h 2.50 · ferry-model.js:604
5. the engine room's Blender model (Cube509) and her metal work share a plane over 644 cm²: they flash
   CONTROL BOOTH · yard 9.85 · x 2.35 S · h 1.90 · ferry-model.js:604
6. the engine room's Blender model (Cube509) and her metal work share a plane over 400 cm²: they flash
   CONTROL BOOTH · yard 10.50 · x 2.35 S · h 2.25 · ferry-model.js:604
7. the engine room's Blender model (Cube509), two of its faces, share a plane over 3.91 m²: they flash
   ENGINE ROOM · yard 11.01 · x 2.11 S · h 1.45
8. the engine room's Blender model (Cube509) and the engine room's Blender model (Cube509_1) share a plane over 239 cm²: they flash
   ENGINE ROOM · yard 11.95 · x 0.37 P · h 1.55
9. the engine room's Blender model (Cube509), two of its faces, share a plane over 4.34 m²: they flash
   ENGINE ROOM · yard 13.48 · x 2.21 S · h 1.52
10. the engine room's Blender model (Cube509) and the engine room's Blender model (Cube509_1) share a plane over 441 cm²: they flash
    ENGINE ROOM · yard 13.72 · x 0.47 S · h 1.24
11. the engine room's Blender model (Cube509), two of its faces, share a plane over 1.88 m²: they flash
    AUX ROOM · yard 17.11 · x 0.84 S · h 1.72
12. the engine room's Blender model (Cube509), two of its faces, share a plane over 5.75 m²: they flash
    AUX ROOM · yard 17.57 · x 1.59 S · h 1.64
13. the engine room's Blender model (Cube509), two of its faces, share a plane over 6131 cm²: they flash
    ENGINE STORE · yard 21.45 · x 2.47 S · h 2.20
14. the engine room's Blender model (Cube509), two of its faces, share a plane over 5805 cm²: they flash
    WORKSHOP · yard 22.08 · x 2.96 P · h 2.28
15. steering-gear: a manned space with 2 exits (steering-gear-hatch, engine-room) but 0% of it can be walked on
    STEERING GEAR · yard 1.45 · x 0.00 P · h 2.05
16. H1 fluorescent fitting rests on nothing and hangs from nothing (its foot 3.40 m above the keel) (in the code-built engine room, seen until the Blender model loads)
    CONTROL BOOTH · yard 9.60 · x 3.10 S · h 3.40 · ferry-interior.js:1303
17. a trim piece stands 16 cm inside main engine (in the code-built engine room, seen until the Blender model loads)
    ENGINE ROOM · yard 10.82 · x ±1.21 · h 1.89 · ferry-interior.js:817, ferry-interior.js:941
18. H1 fluorescent fitting rests on nothing and hangs from nothing (its foot 3.40 m above the keel) (in the code-built engine room, seen until the Blender model loads)
    AUX ROOM · yard 15.50 · x 0.00 P · h 3.40 · ferry-interior.js:1303
19. H1 fluorescent fitting rests on nothing and hangs from nothing (its foot 3.40 m above the keel) (in the code-built engine room, seen until the Blender model loads)
    AUX ROOM · yard 18.00 · x 0.00 P · h 3.40 · ferry-interior.js:1303
20. H1 fluorescent fitting rests on nothing and hangs from nothing (its foot 3.40 m above the keel) (in the code-built engine room, seen until the Blender model loads)
    WORKSHOP · yard 21.00 · x 1.70 P · h 3.40 · ferry-interior.js:1303

… and 3 more: issues.json

NOTES


Drawn from buildFerryModel() as the game builds it: plans are cut by a horizontal plane and sections by a vertical one, and what is cut is drawn heavy, what lies beyond in outline. The design (general arrangement, ferry-ship.js) is dashed over each plan: a room built away from its design shows.

Issues are found in her data by tools/ferry-audit.mjs and numbered for the whole set: red a clash, amber a check. Their source lines are in issues.json.

YARD Johansson Shipyard, Innoshima **JOHANSSON SHIPYARD**	SHIP M/V MINATO MARU hull No. 127, built 1994	DRAWING No. **JS-127-C3**
TITLE ENGINE ROOM AND MACHINERY SPACES **Steering gear, shaft space, engine room, auxiliary room, workshops, bow thruster**		SCALE 1:50 on A1
SOURCE tools/ferry-cad.mjs	DATA buildFerryModel() as built	STATUS WORKING DRAWING
SHEET 3 / 8	DRAWN Claude, AI survey	CHECKED owner review open
DATE 2026-11-09	REV C · working set by section	


WHEELHOUSE AND WINGS · plan cut 1.5 m above the deck

SCALE 1:25

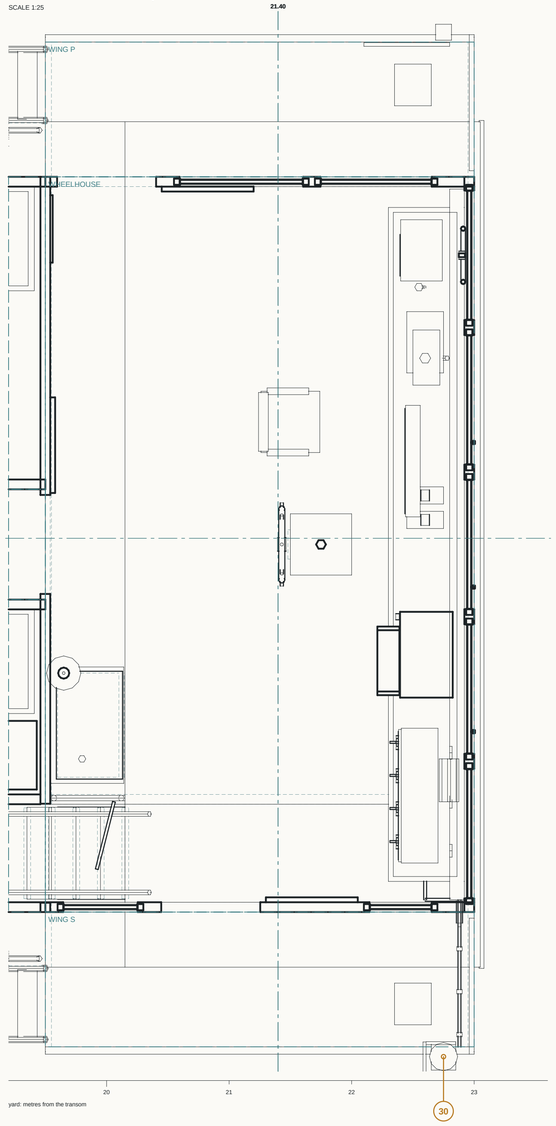


AT 21.4 · LOOKING FORWARD

SCALE 1:25

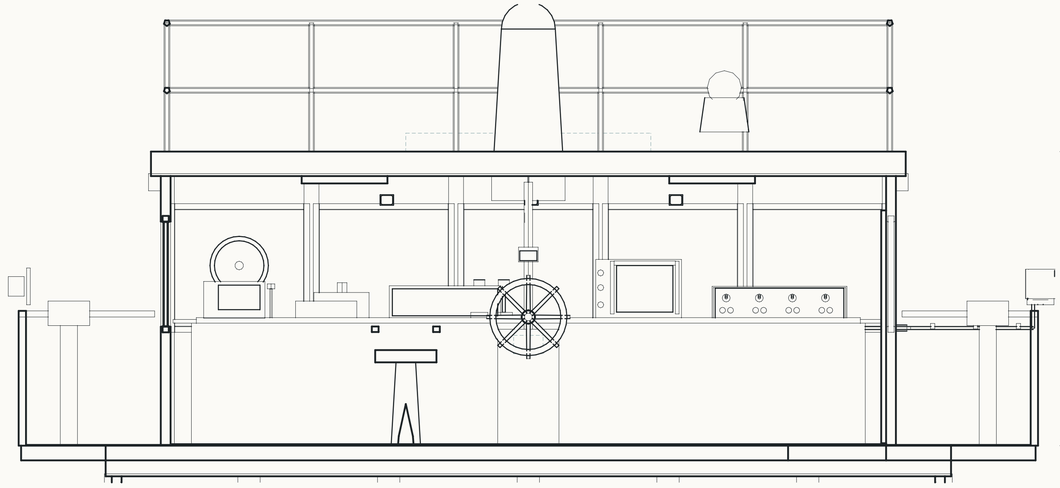


AT 21.4 · LOOKING AFT

SCALE 1:25

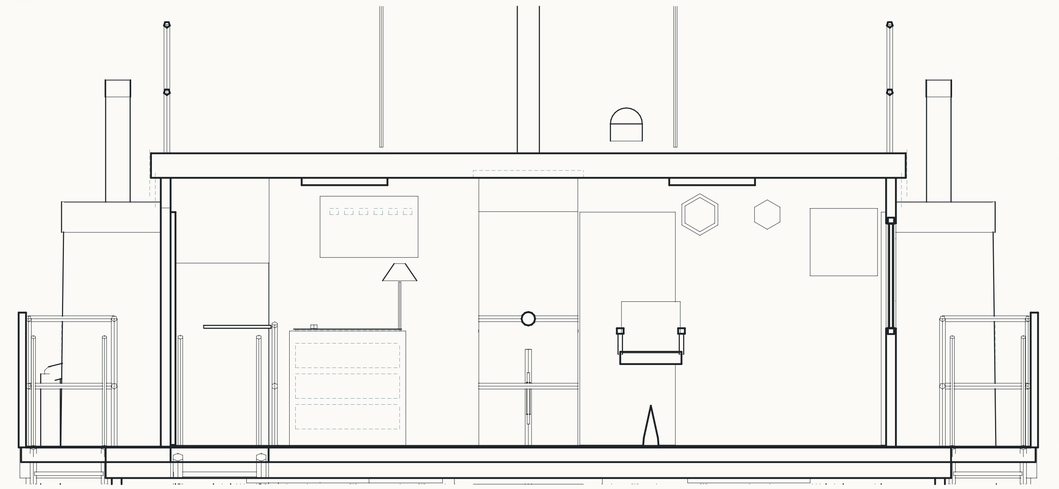


ON THE CENTRELINE · looking to port

SCALE 1:25

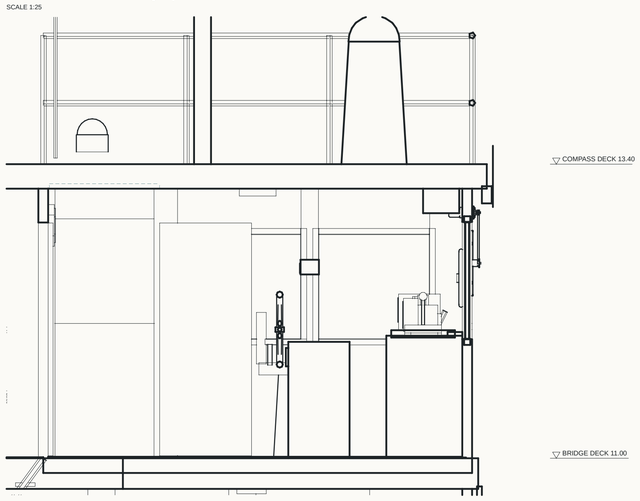

COMPASS DECK FROM ABOVE

SCALE 1:50

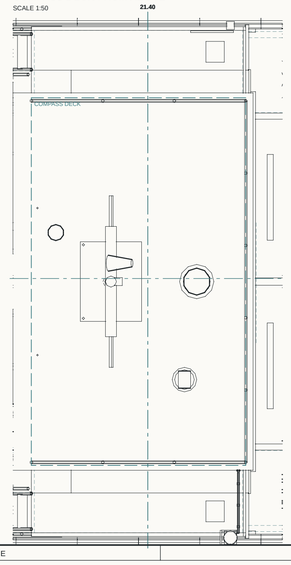

ISSUES IN THIS SECTION · 0 clash, 1 check

30 Navigation feeder fallback › Navigation panel, protection and actual two-core cable, two of its faces, share a plane over 15 cm²: they flash
WING S · yard 22.75 › x 4.18 S › h 12.15

DESIGN AND AS BUILT

The general arrangement's words (ferry-ship.js), then the named fittings built in the room (ferry-interior.js).

WHEELHOUSE

Design: Wheelhouse: the steering stand (wheel, non-follow-up lever, autopilot); two engine levers and the thruster lever at the centre and on both wing consoles; the radar; the magnetic compass periscope; VHF with DSC; the ship's telephone; the NAVTEX printer; the echo sounder; the GPS display; the chart table with its drawers and red lamp; the navigation-light panel; the fire panel; the PA and general alarm; the ramp lamps; the whistle button; the searchlight control; the wipers; a clock, a barometer, an inclinometer; the log desk; the master's high chair
Built: wing door ×2, wheelhouse console, steering stand, chart table

WING P

Design: Bridge wing, port, open: a wing console with the engine and thruster levers, the port sidelight at its end
Built: no named fittings

WING S

Design: Bridge wing, starboard, open: a wing console, the starboard sidelight at its end, the float-free EPIRB
Built: no named fittings

COMPASS DECK

Design: Compass deck: the standard magnetic compass, the mast with the radar scanner on its platform, the masthead light at 15 m, the all-round lights, the whistle, the VHF and GPS antennas, the searchlight, the company flag
Built: no named fittings

NOTES

Drawn from buildFerryModel() as the game builds it: plans are cut by a horizontal plane and sections by a vertical one, and what is cut is drawn heavy, what lies beyond in outline. The design (general arrangement, ferry-ship.js) is dashed over each plan: a room built away from its design shows.


Issues are found in her data by tools/ferry-audit.mjs and numbered for the whole set: red a clash, amber a check. Their source lines are in issues.json.

YARD Johansson Shipyard, Innoshima **JOHANSSON SHIPYARD**		SHIP M/V MINATO MARU hull No. 127, built 1994	DRAWING No. **JS-127-C4**
TITLE BRIDGE · wheelhouse, wings and compass deck **Consoles, steering stand, chart table, crew stair well, wing consoles**			SCALE 1:25 1:50 compass deck
SOURCE tools/ferry-cad.mjs	DATA buildFerryModel() as built	STATUS WORKING DRAWING	SHEET 4 / 8
DRAWN Claude, AI survey	CHECKED owner review open	DATE 2026-11-09	REV C · working set by section

WORKING DRAWINGS OF THE GAME MODEL · Johansson World vessel · no flag, class or construction approval · buildFerryModel() as built, cut and drawn with hidden lines removed · issues from tools/ferry-audit.mjs

PASSENGER DECK · plan cut 1.5 m above it


SCALE 1:50

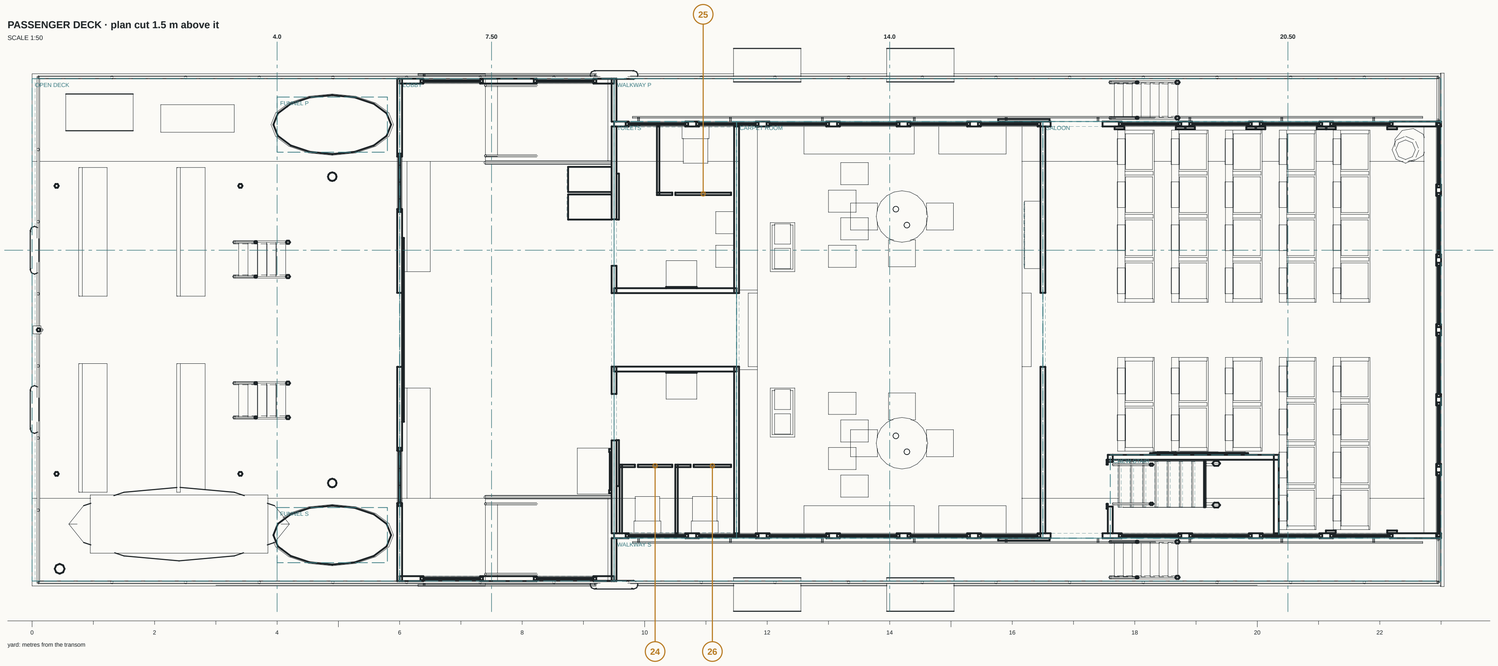

yard: metres from the transom

SECTION AT 1.3 TO PORT · looking to port


SCALE 1:50

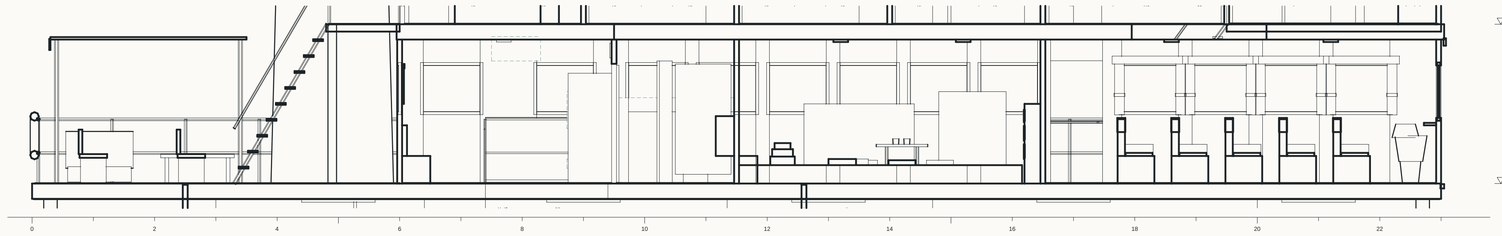

yard: metres from the transom


AT 7.5 · LOBBY

SCALE 1:50

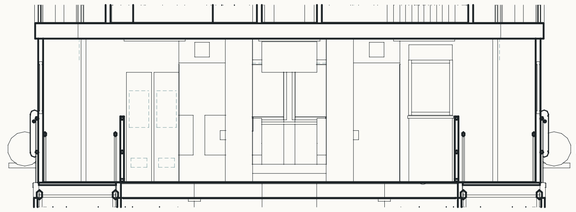


AT 14.0 · CARPET ROOM

SCALE 1:50

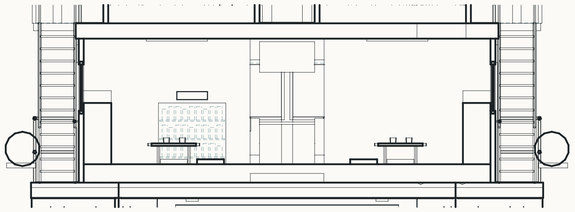


AT 20.5 · SALOON

SCALE 1:50

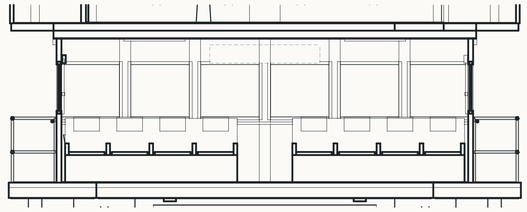

AT 4.0 · OPEN DECK

SCALE 1:50

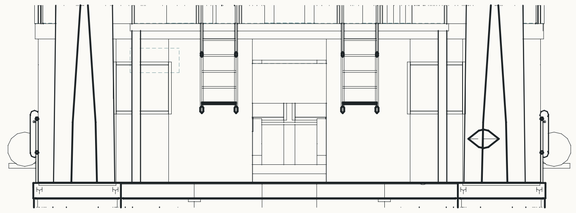

ISSUES IN THIS SECTION · 0 clash, 3 check

24 cubicle door rests on nothing and hangs from nothing (its foot 8.55 m above the keel)
TOILETS · yard 10.17 · x 2.22 S · h 8.55 · ferry-interior.js:360

25 cubicle door rests on nothing and hangs from nothing (its foot 8.55 m above the keel)
TOILETS · yard 10.95 · x 2.22 P · h 8.55 · ferry-interior.js:360

26 cubicle door rests on nothing and hangs from nothing (its foot 8.55 m above the keel)
TOILETS · yard 11.11 · x 2.22 S · h 8.55 · ferry-interior.js:360

NOTES


Drawn from buildFerryModel() as the game builds it: plans are cut by a horizontal plane and sections by a vertical one, and what is cut is drawn heavy, what lies beyond in outline. The design (general arrangement, ferry-ship.js) is dashed over each plan: a room built away from its design shows.

Issues are found in her data by tools/ferry-audit.mjs and numbered for the whole set: red a clash, amber a check. Their source lines are in issues.json.

YARD Johansson Shipyard, Innoshima **JOHANSSON SHIPYARD**	SHIP MV MINATO MARU hull No. 127, built 1994	DRAWING No. **JS-127-C5**
TITLE PASSENGER ACCOMMODATION **Open deck, lobby, toilets, carpet room, saloon, walkways, crew stair**		SCALE 1:50 on A1
SOURCE tools/ferry-cad.mjs	DATA buildFerryModel() as built	STATUS WORKING DRAWING	SHEET 5 / 8
DRAWN Claude, AI survey	CHECKED owner review open	DATE 2026-11-09	REV C · working set by section

BRIDGE DECK · plan cut 1.5 m above it


SCALE 1:50

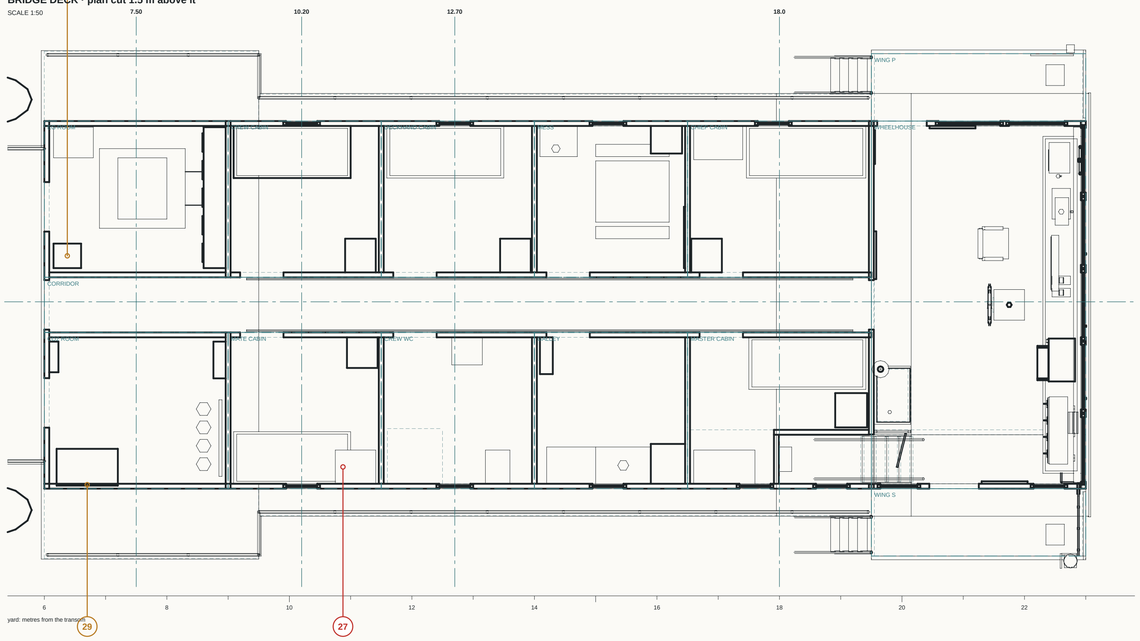

yard: metres from the transom

SECTION ON THE CENTRELINE · the corridor, looking to port


SCALE 1:50

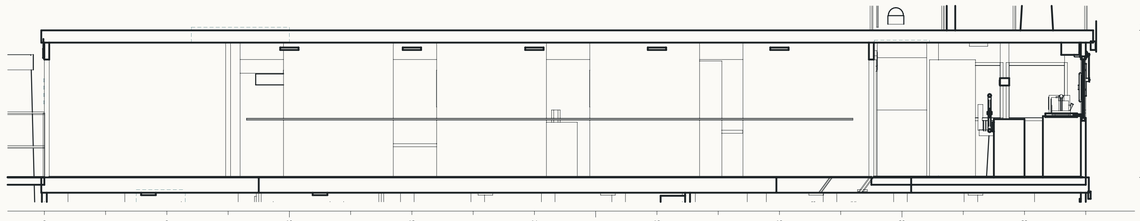

yard: metres from the transom


AT 7.5 · EG AND CO2 ROOMS

SCALE 1:50

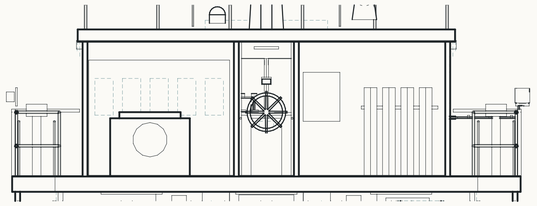


AT 10.2 · CREW AND MATE'S CABINS

SCALE 1:50

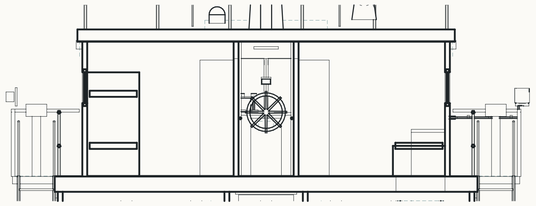


AT 12.7 · DECKHAND'S CABIN, CREW WC

SCALE 1:50

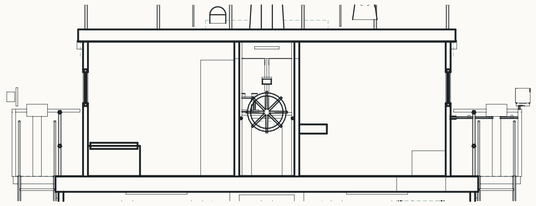

AT 18.0 · CHIEF'S AND MASTER'S CABINS

SCALE 1:50

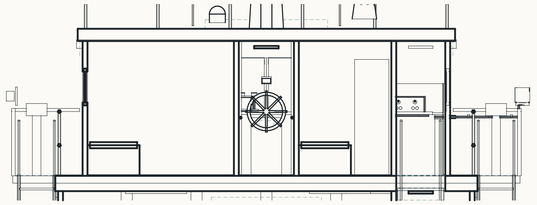

ISSUES IN THIS SECTION · 1 clash, 2 check

27 bunk and desk occupy the same space, 25 cm deep
MATE CABIN · yard 10.88 › x 2.65 S · h 11.25 · ferry-interior.js:681, ferry-interior.js:684

28 day tank rests on nothing and hangs from nothing (its foot 12.30 m above the keel)
EG ROOM · yard 6.28 › x 0.80 P · h 12.30 · ferry-interior.js:670

29 fireman's outfit locker runs 3 cm into a wall or deck
CO2 ROOM · yard 6.70 · x 2.94 S · h 11.95 · ferry-interior.js:677, ferry-interior.js:631

DESIGN AND AS BUILT

The general arrangement's words (ferry-ship.js), then the named fittings built in the room (ferry-interior.js).

EG ROOM
Design: Emergency-generator room: the 40 kVA emergency generator, the emergency switchboard, the 24 V batteries and their chargers, a 60 L day tank, louvres
Built: emergency generator, emergency switchboard, battery box, day tank

CO2 ROOM
Design: CO_2 room and fire-control station: four 45 kg CO_2 bottles, the release cabinet, the remote fan stops and fuel quick-closing valves, two firemen's outfits
Built: CO_2 release cabinet, fireman's outfit locker, fan stops

CREW CABIN
Design: Crew cabin, two berths: the bosun and the oiler; bunk beds, lockers, a fold-down desk
Built: bunk, locker

MATE CABIN
Design: Chief officer's cabin
Built: bunk, desk ×2, locker

DECKHAND CABIN
Design: Deckhand's cabin
Built: bunk, locker

CHIEF CABIN
Design: Johansson's chief engineer duty cabin
Built: bunk, desk ×2, locker

MASTER CABIN
Design: Master's cabin: a desk, a bunk along the corridor's wall, the ship's papers and the safe; the crew stair's trunk walled off in its outboard forward corner
Built: bunk, desk ×2, safe, locker

CORRIDOR
Design: The crew's corridor down the middle, from their own door aft onto the bridge deck's platform (they come up the open deck's ladders) to the wheelhouse
Built: no named fittings

NOTES


Drawn from buildFerryModel() as the game builds it: plans are cut by a horizontal plane and sections by a vertical one, and what is cut is drawn heavy, what lies beyond in outline. The design (general arrangement, ferry-ship.js) is dashed over each plan: a room built away from its design shows.

Issues are found in her data by tools/ferry-audit.mjs and numbered for the whole set: red a clash, amber a check. Their source lines are in issues.json.

YARD Johansson Shipyard, Innoshima **JOHANSSON SHIPYARD**	SHIP MV MINATO MARU hull No. 127, built 1994		DRAWING No. **JS-127-C6**
TITLE CREW ACCOMMODATION · the bridge deck house **Emergency generator and CO2 rooms, cabins, crew WC, mess, galley, corridor**			SCALE 1:50 on A1
SOURCE tools/ferry-cad.mjs	DATA buildFerryModel() as built	STATUS WORKING DRAWING	SHEET 6 / 8
DRAWN Claude, AI survey	CHECKED owner review open	DATE 2026-11-09	REV C · working set by section


PASSENGERS' TOILETS · plan 1.5 m above the deck

SCALE 1:25

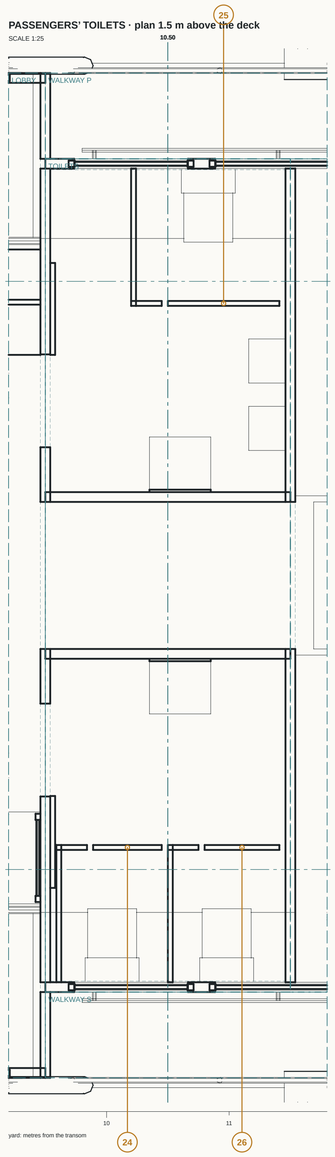


AT 10.5 · LOOKING FORWARD

SCALE 1:25

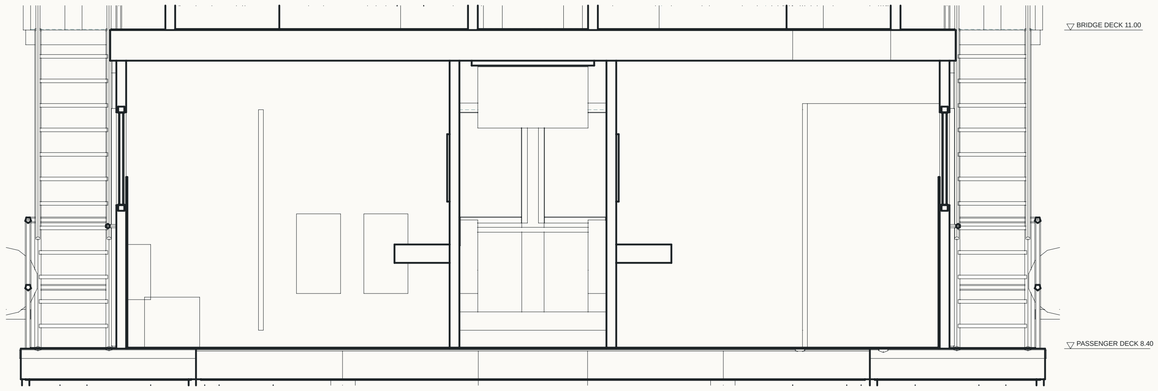


AT 10.5 · LOOKING AFT

SCALE 1:25

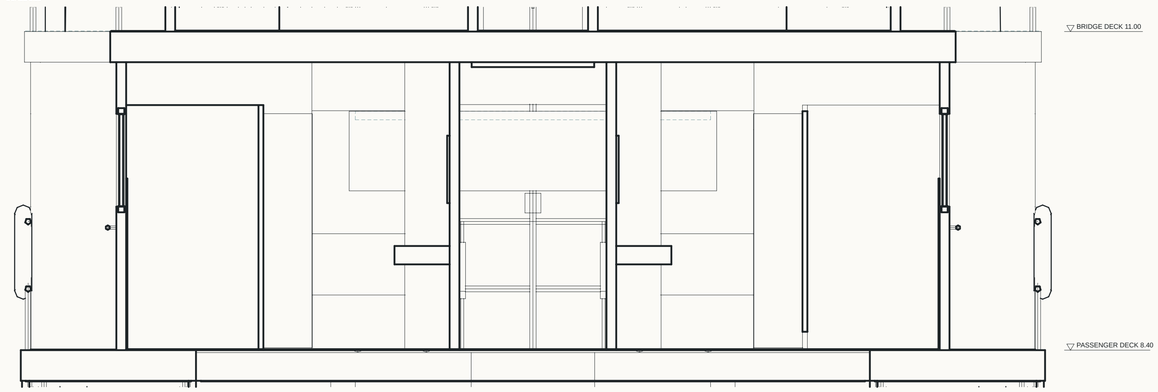


MEN'S · AT 2.4 TO PORT

SCALE 1:25

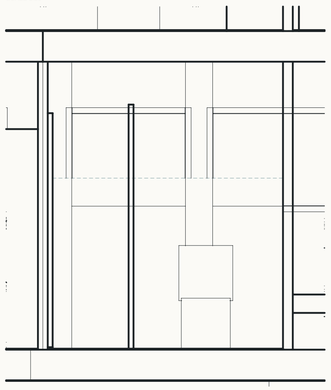


WOMEN'S · AT 2.4 TO STBD

SCALE 1:25

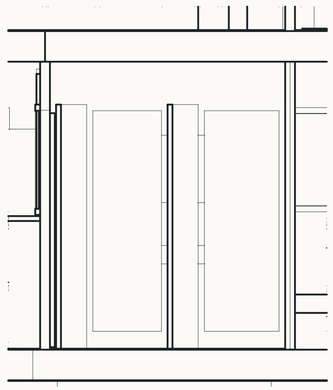


CREW WC · AT 12.7 LOOKING FWD

SCALE 1:25

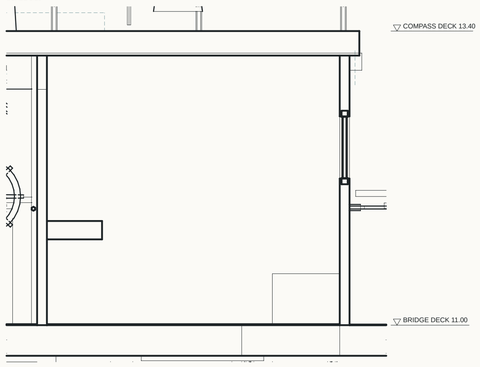

CREW WC · plan

SCALE 1:25

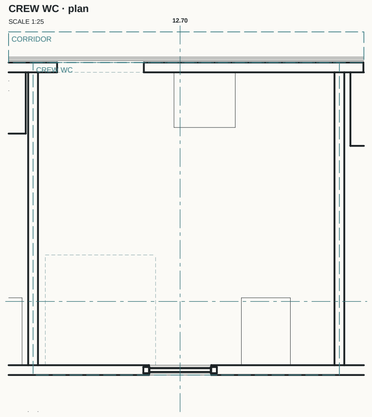

ISSUES IN THIS SECTION · 0 clash, 3 check

24 cubicle door rests on nothing and hangs from nothing (its foot 8.55 m above the keel)
TOILETS · yard 10.17 · x 2.22 S · h 8.55 · ferry-interior.js:360

25 cubicle door rests on nothing and hangs from nothing (its foot 8.55 m above the keel)
TOILETS · yard 10.95 · x 2.22 P · h 8.55 · ferry-interior.js:360

26 cubicle door rests on nothing and hangs from nothing (its foot 8.55 m above the keel)
TOILETS · yard 11.11 · x 2.22 S · h 8.55 · ferry-interior.js:360

DESIGN AND AS BUILT

The general arrangement's words (ferry-ship.js), then the named fittings built in the room (ferry-interior.js).

TOILETS
Design: Toilets: men's to port (a WC, two urinals, a basin), women's to starboard (two WCs, a basin); sea-water flushing
Built: basin ×2, cubicle partition ×6, cubicle door ×3, WC ×3, cistern ×3, urinal ×2

CREW WC
Design: Crew WC and shower
Built: WC, basin

NOTES


Drawn from buildFerryModel() as the game builds it: plans are cut by a horizontal plane and sections by a vertical one, and what is cut is drawn heavy, what lies beyond in outline. The design (general arrangement, ferry-ship.js) is dashed over each plan: a room built away from its design shows.

Issues are found in her data by tools/ferry-audit.mjs and numbered for the whole set: red a clash, amber a check. Their source lines are in issues.json.

YARD Johansson Shipyard, Innoshima **JOHANSSON SHIPYARD**		SHIP M/V MINATO MARU hull No. 127, built 1994	DRAWING No. **JS-127-C7**
TITLE TOILETS · passengers' and crew **Men's to port, women's to starboard; the crew WC and shower**			SCALE 1:25 on A1
SOURCE tools/ferry-cad.mjs	DATA buildFerryModel() as built	STATUS WORKING DRAWING	SHEET 7 / 8
DRAWN Claude, AI survey	CHECKED owner review open	DATE 2026-11-09	REV C · working set by section

GALLEY AND MESS · plan 1.5 m above the deck


SCALE 1:25

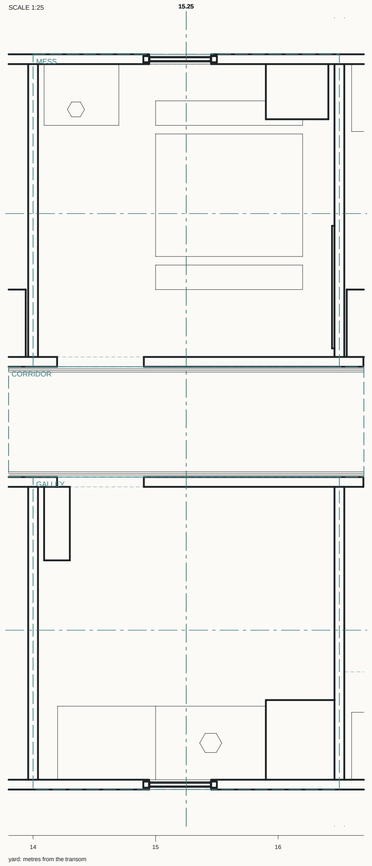

yard: metres from the transom


AT 15.25 · LOOKING FORWARD

SCALE 1:25

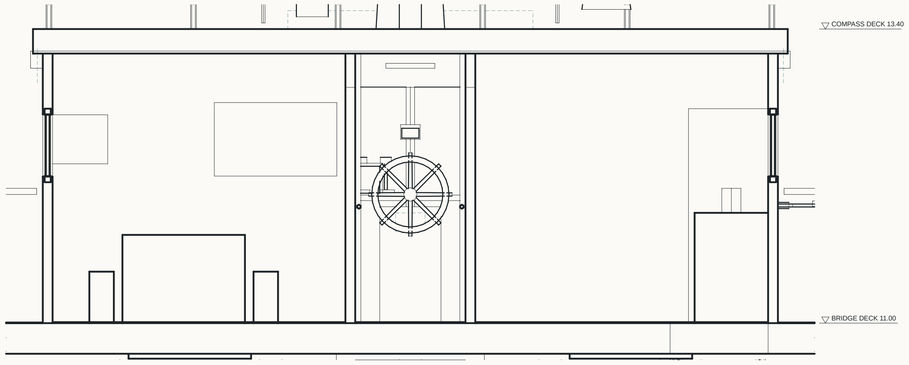


AT 15.25 · LOOKING AFT

SCALE 1:25

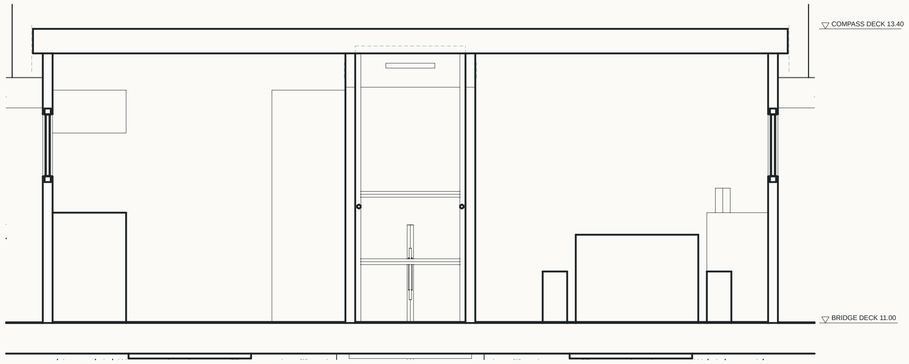


GALLEY · AT 1.7 TO STBD

SCALE 1:25

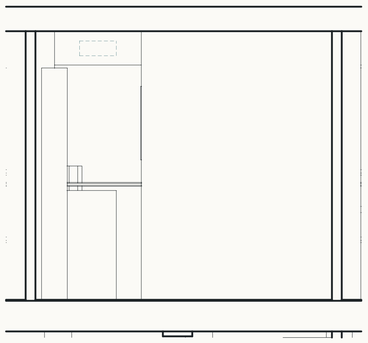

MESS · AT 1.7 TO PORT

SCALE 1:25

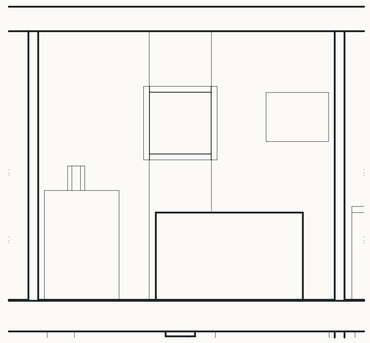

ISSUES IN THIS SECTION · 0 clash, 0 check

None found by the audit. What it cannot see (a door in the wrong place, a missing handrail, a room wrong for its use) is for the owner's review of the drawing.

DESIGN AND AS BUILT

The general arrangement's words (ferry-ship.js), then the named fittings built in the room (ferry-interior.js).

GALLEY

Design: Galley: a three-plate range, the rice cooker, a fridge-freezer, a sink, a hood, the provision locker, a hatch to the mess
Built: range, hood, sink, fridge-freezer, provision locker

MESS

Design: Mess room: a table for six, a television, a kettle, the duty board and the muster list
Built: mess table, mess bench ×2, mess television, sideboard

NOTES

Drawn from buildFerryModel() as the game builds it: plans are cut by a horizontal plane and sections by a vertical one, and what is cut is drawn heavy, what lies beyond in outline. The design (general arrangement, ferry-ship.js) is dashed over each plan: a room built away from its design shows.

Issues are found in her data by tools/ferry-audit.mjs and numbered for the whole set: red a clash, amber a check. Their source lines are in issues.json.

YARD	SHIP	DRAWING No.
Johansson Shipyard, Innoshima **JOHANSSON SHIPYARD**	M/V MINATO MARU hull No. 127, built 1994	**JS-127-C8**
TITLE		SCALE
GALLEY AND MESS **The crew's galley to starboard and mess room to port, on the bridge deck**		1:25 on A1
SOURCE	DATA	STATUS / SHEET
tools/ferry-cad.mjs	buildFerryModel() as built	WORKING DRAWING · 8 / 8
DRAWN	CHECKED	DATE / REV
Claude, AI survey	owner review open	2026-11-09 · C - working set by section