
General arrangement

Clear dimensions in millimetres. Plan at 1:50 on A3; do not scale a resized print.

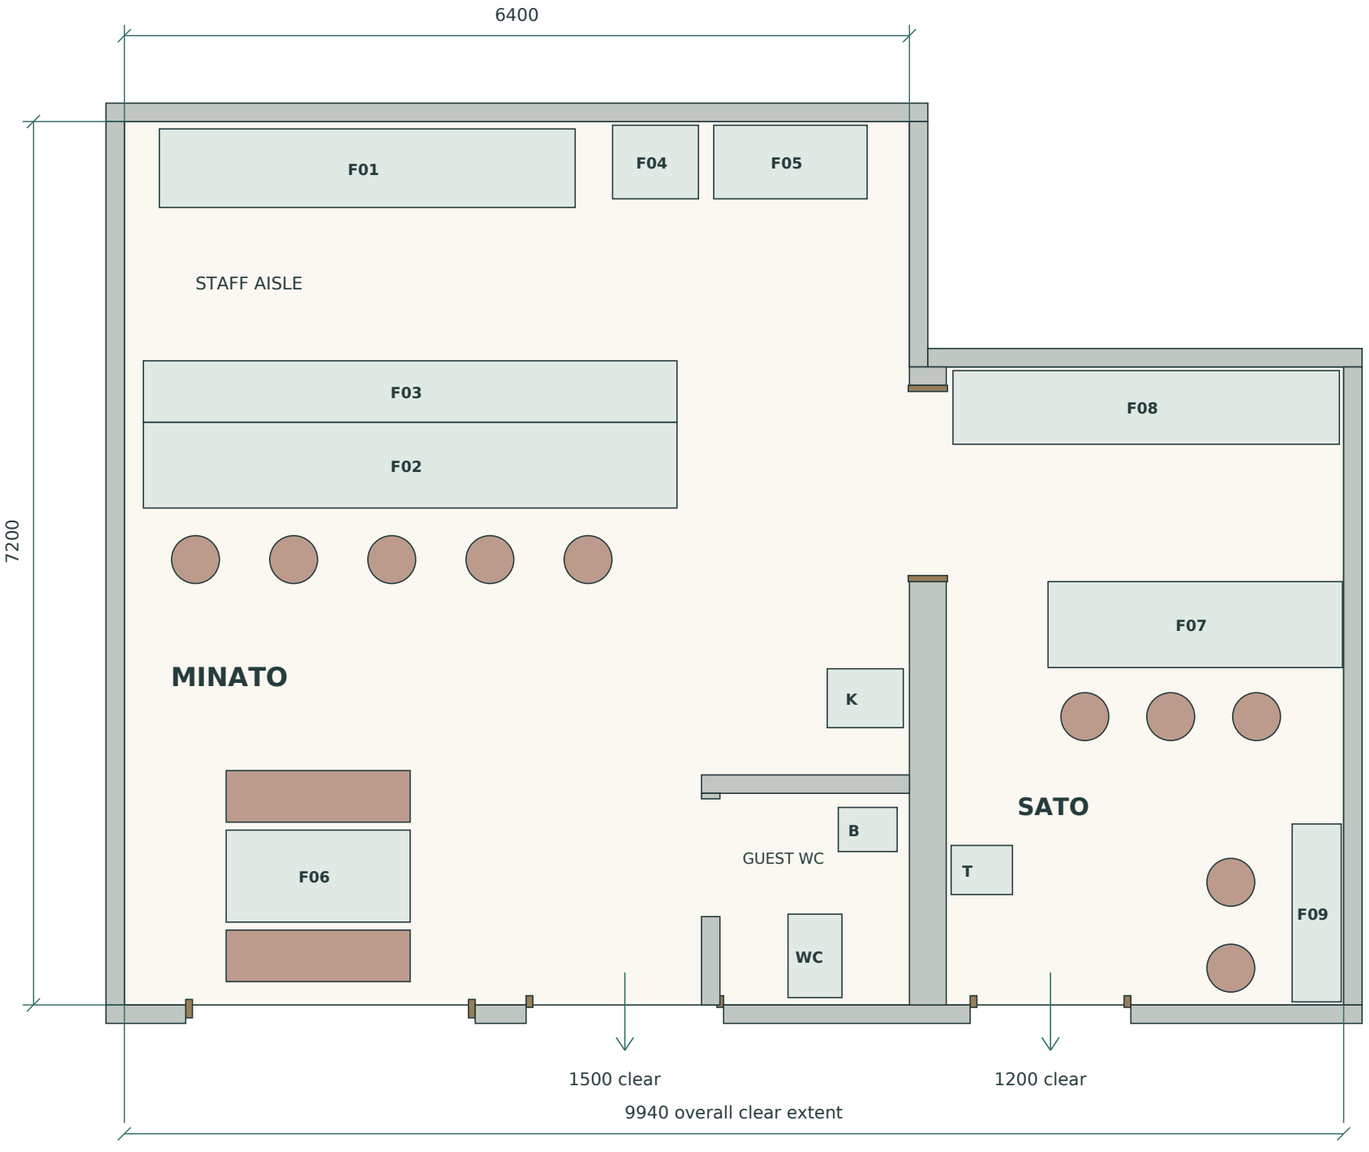

Drawing keys

F01 Original walnut cabinet, 3390 x 640

F02 Guest counter, 4350 x 700

F03 Service worktop, 4350 x 500

F04 Cold store, 700 x 600

F05 Wash / cooking unit, 1250 x 600

F06 Four-place table, 1500 x 750

F07 Sato counter, 2400 x 700

F08 Sato prep bench, 3150 x 600

F09 Side ledge, 400 x 1450

K Karaoke T Meal tickets B Basin

Clear circulation

Minato staff aisle: 1250

Sato working aisle: 1120

Shared passage: 1500 clear

Guest WC door: 860 clear

5 Minato stools + 4 booth places

3 Sato stools + 2 ledge places


The two street doors enter one connected restaurant. Existing seats, serving points and circulation are retained.

Rough openings include their timber frames. Walls stop at the outside of the joinery; window corners use butt joints.

Furniture footprints are measured envelopes. Game collision margins are checked separately by the regression suite.

Service section and joinery

Service section at 1:30 on A3. Heights use the game Y datum; the finished floor is Y = 40 mm.

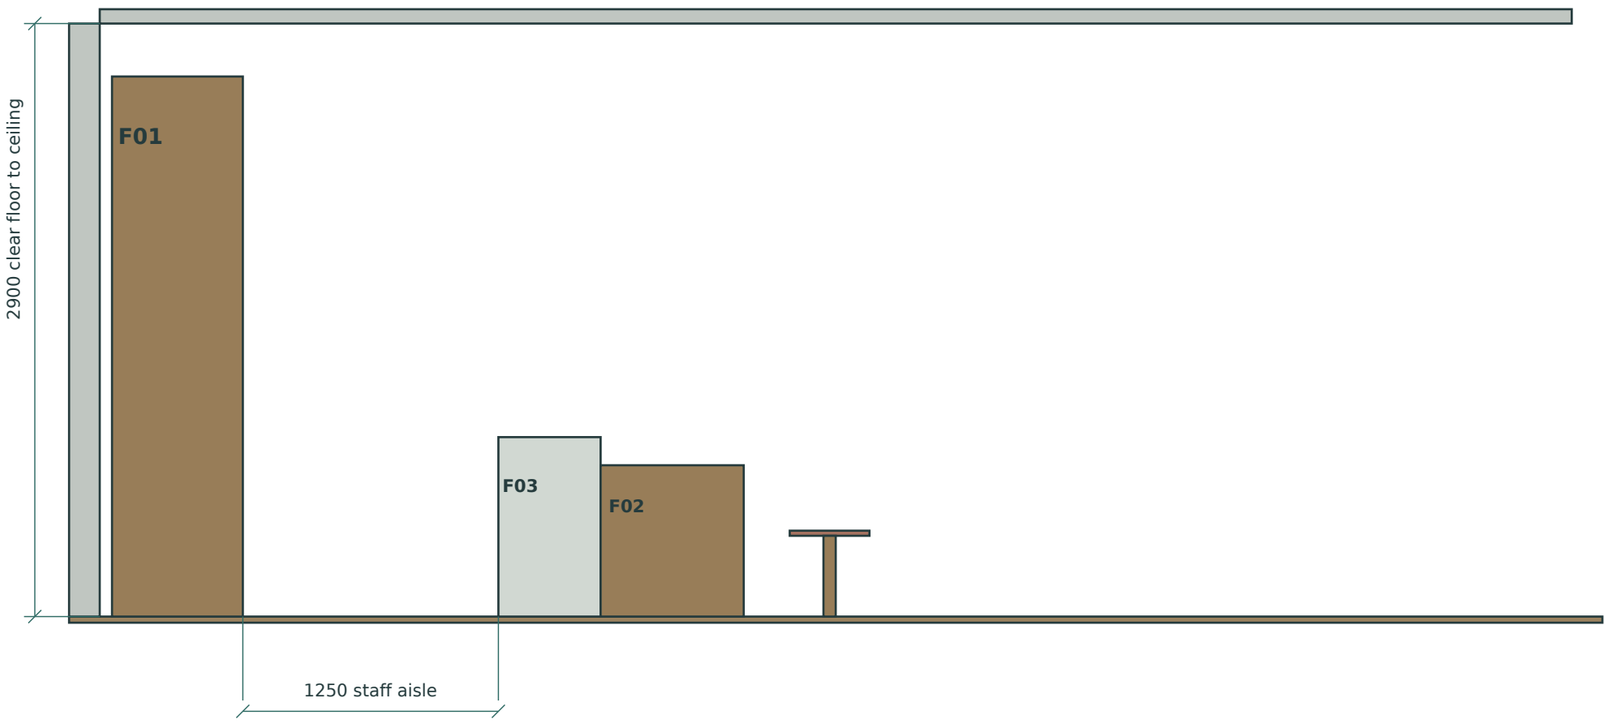

Height schedule / Y datum

Ceiling underside 2940

Cabinet top 2681 (export rounded)

Kitchen worktop 917.5

Guest / Sato counter 780

Booth table 720

Stool / bench seat 460

Finished floor 40

Repair details

Printed book and recipe faces are part of their solid surfaces.

Food sits inside open topping pans.

Can artwork is the metal sidewall.

Appliance radii fit the panel height.

Washroom lettering faces the room.

Joinery dimensions

Minato door: 1500 clear + 2 x 55 jambs = 1610 rough width; head allowance 75.

Street window: 2250 x 1050 clear; 55 frame gives a 2360 x 1160 rough aperture.

Kitchen link: 1500 clear + 2 x 50 jambs = 1600 rough opening; head allowance 70.

Guest WC: 860 clear + 2 x 50 jambs = 960 rough opening; folding leaves remain parked clear.

Stool projected from the nearest counter place. Existing seat heights are preserved; this is a geometric game drawing.

Architectural review

Blender 4.5.3 LTS render of the rebuilt source. This is not a running-game or physical-device screenshot.





Sango Quay / Artlist

Original fictional house-brand print.

Seedream 4.5, 30 October 2026.

Mounted once by the game; the

Blender copy is review-only.

Measured check: 0 closed-door and 0 open-door surface conflicts at 2 mm / 0.0005 m2.

The full fitted interior, runtime dressing and material geometry are scanned. A planted wall overlay must still fail.

The reported device crash is not reproduced here. Entry failure now returns outside and records the original error.