Small shop. Very loud posters.


Finished artwork / Kogane chips, Hamabe senbei and hot oden / A2 portrait 420 x 594 mm



P01 Kogane / Snack emergency

420 x 594 mm / matte paper / taped or framed

No invented discounts or changed packaging.

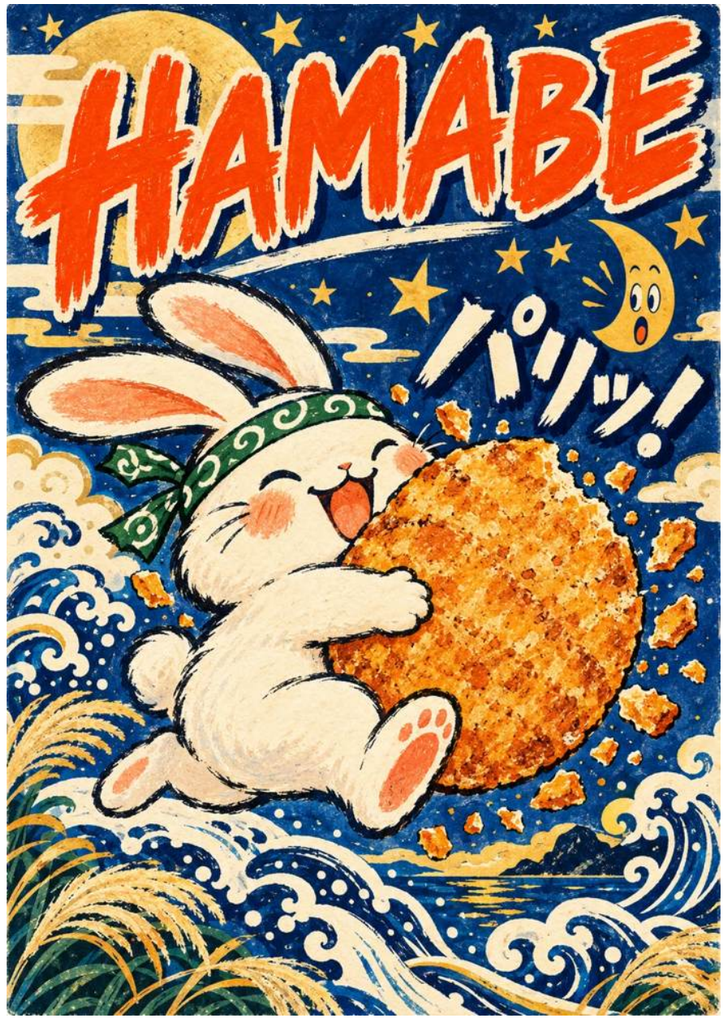

P02 Hamabe / Moon rabbit

420 x 594 mm / matte paper / taped or framed

No invented discounts or changed packaging.



P03 Oden dance

420 x 594 mm / matte paper / taped or framed

No invented discounts or changed packaging.

Tissue Diva

An adult fictional model makes ordinary facial tissues look absurdly luxurious.



P04 / A2 / 420 x 594 mm

For onions. For heartbreak. For everything.

A straight-faced 1990s glamour advertisement for a real Sakura catalogue category: tissues.

Original adult model and illustrated onion. No real celebrity, medical claim, price or sale promise.


Proposed on the west wall near the front magazines, above their top and before the fresh-food chiller.

All four artworks were generated with the built-in image tool. Complete prompts and asset provenance are included with the drawing files.

Poster placement / measured wall elevations

A2 full artwork in the available wall zones / all heights above finished floor / units mm

EAST / south at left, north at right / 1:30.8 at A3

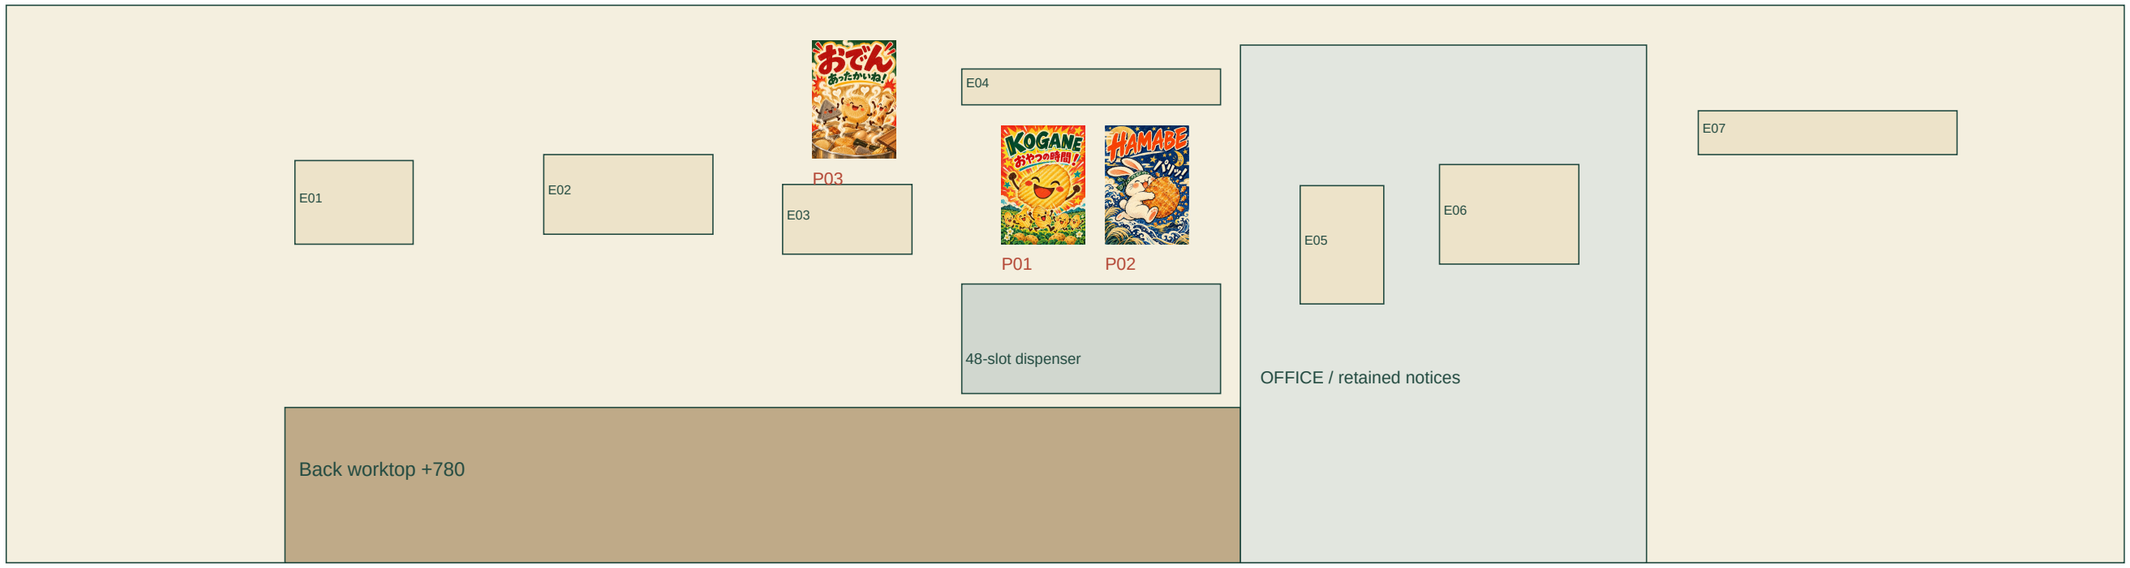



WEST / front corner detail

P01: depth 5000-5420 / height 1600-2194

P02: depth 5520-5940 / height 1600-2194


P03: depth 4050-4470 / height 2030-2624

P04: depth 300-720 / height 1300-1894

No poster overlaps a retained wall notice. All tops below +2800 ceiling. Door, observation glazing, chiller air path and price tickets remain protected.

Counter wall / combined effect

CAD axonometric with the actual poster artwork - a coordination view, not a game screenshot

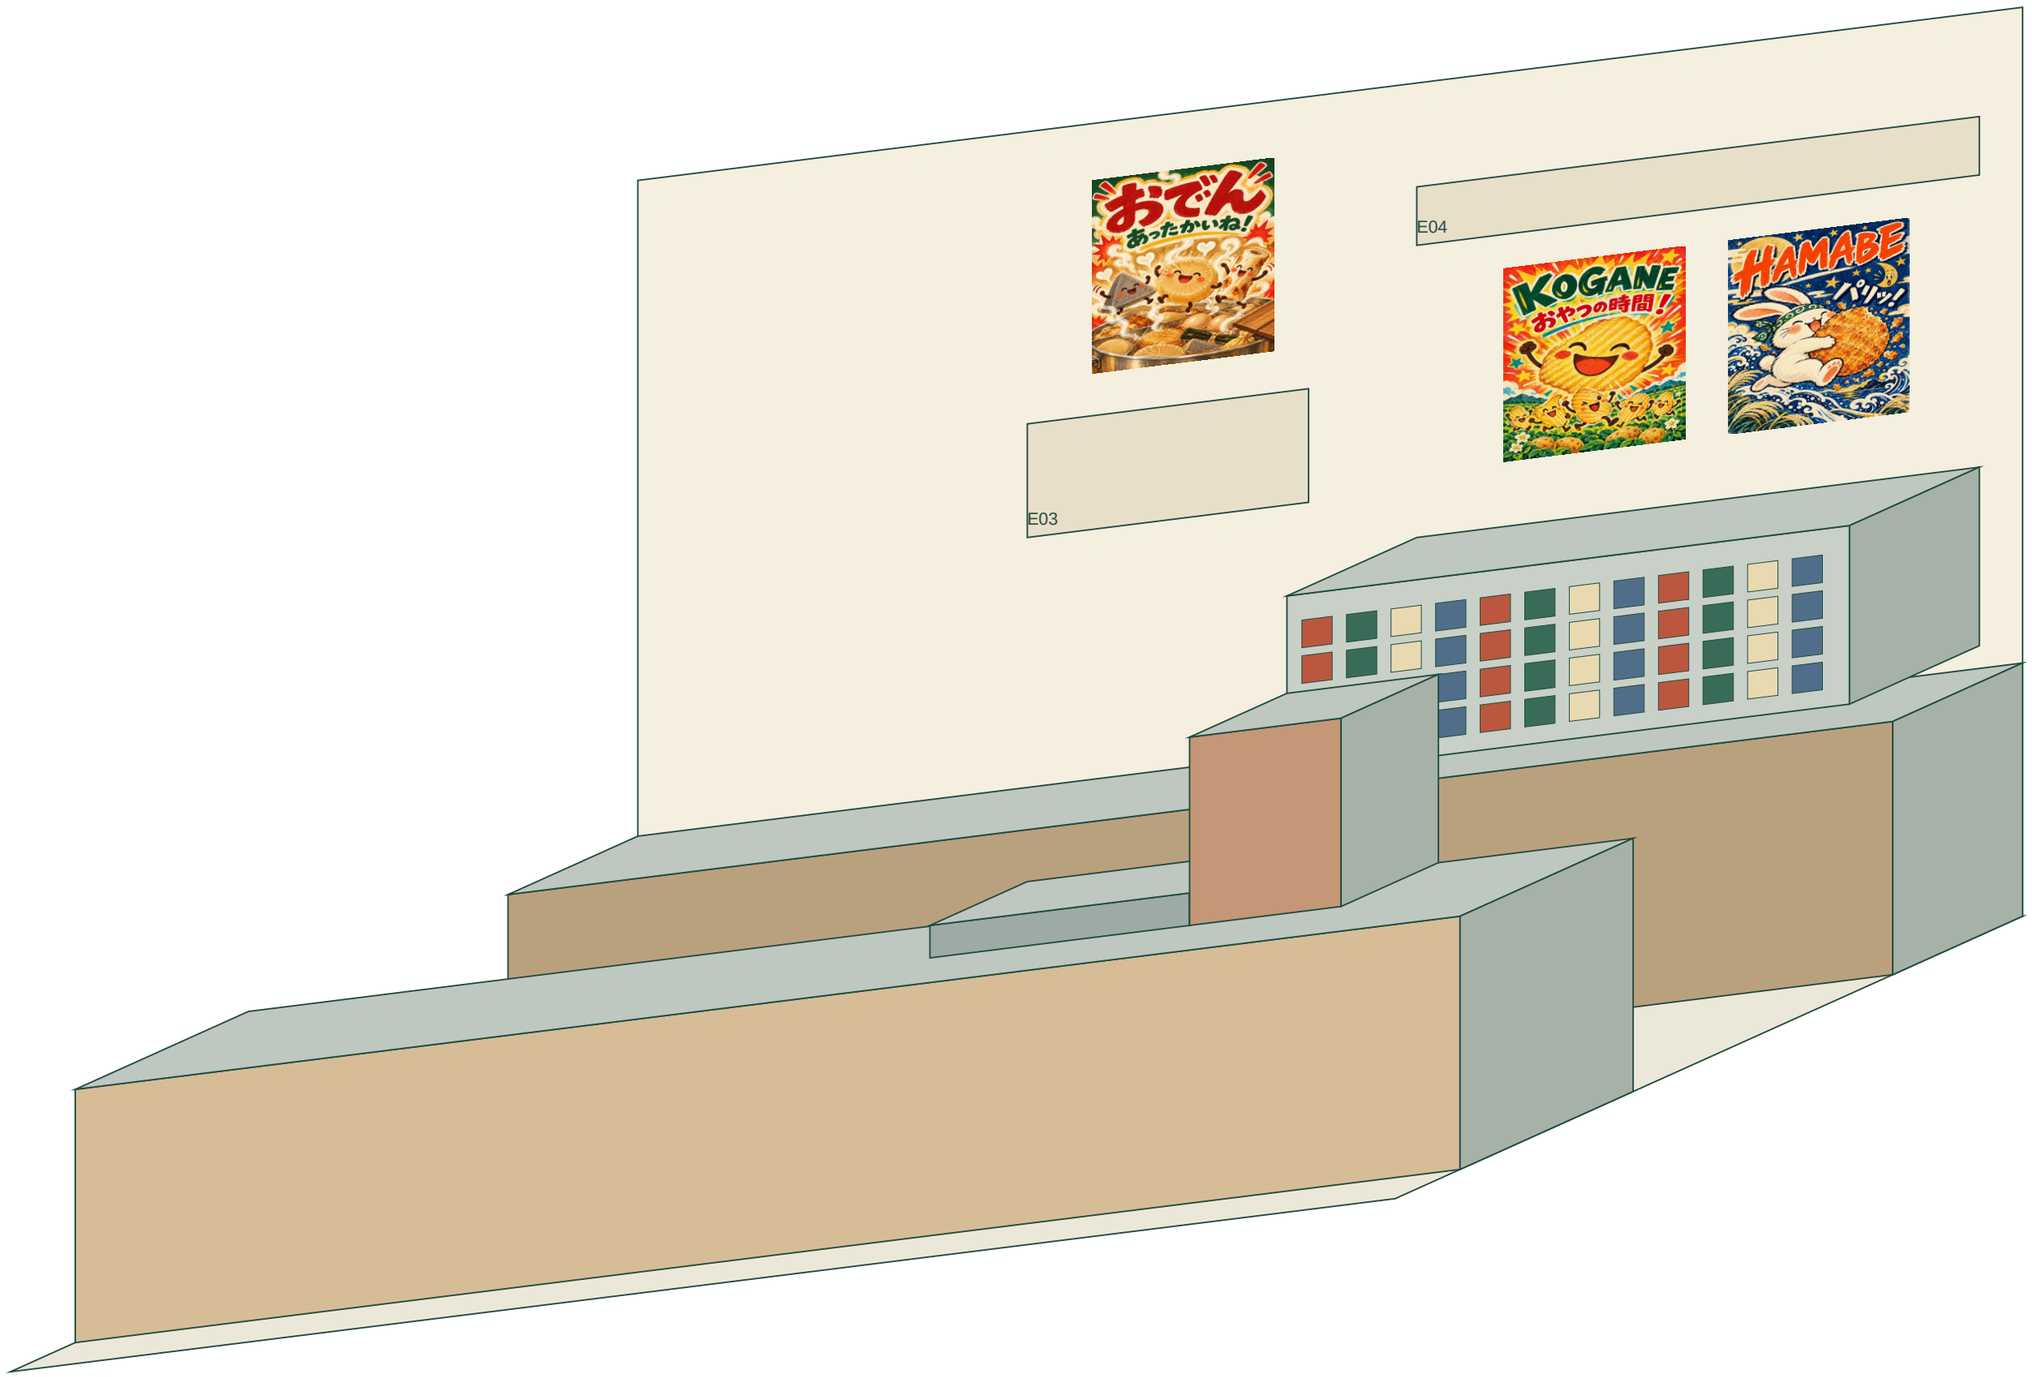


Artwork sits above equipment; original service/hygiene notices and tobacco header are retained.

Realistic A2 poster sizes: 420 x 594 mm. The original product packaging stays intact.

Coordination drawing only; no runtime products, character reach, stock counts or collisions changed.

Roof plan / tank, access and service route

Fixed 14260 x 11000 mm exterior / deck +4010 / one storey / roof-only stair

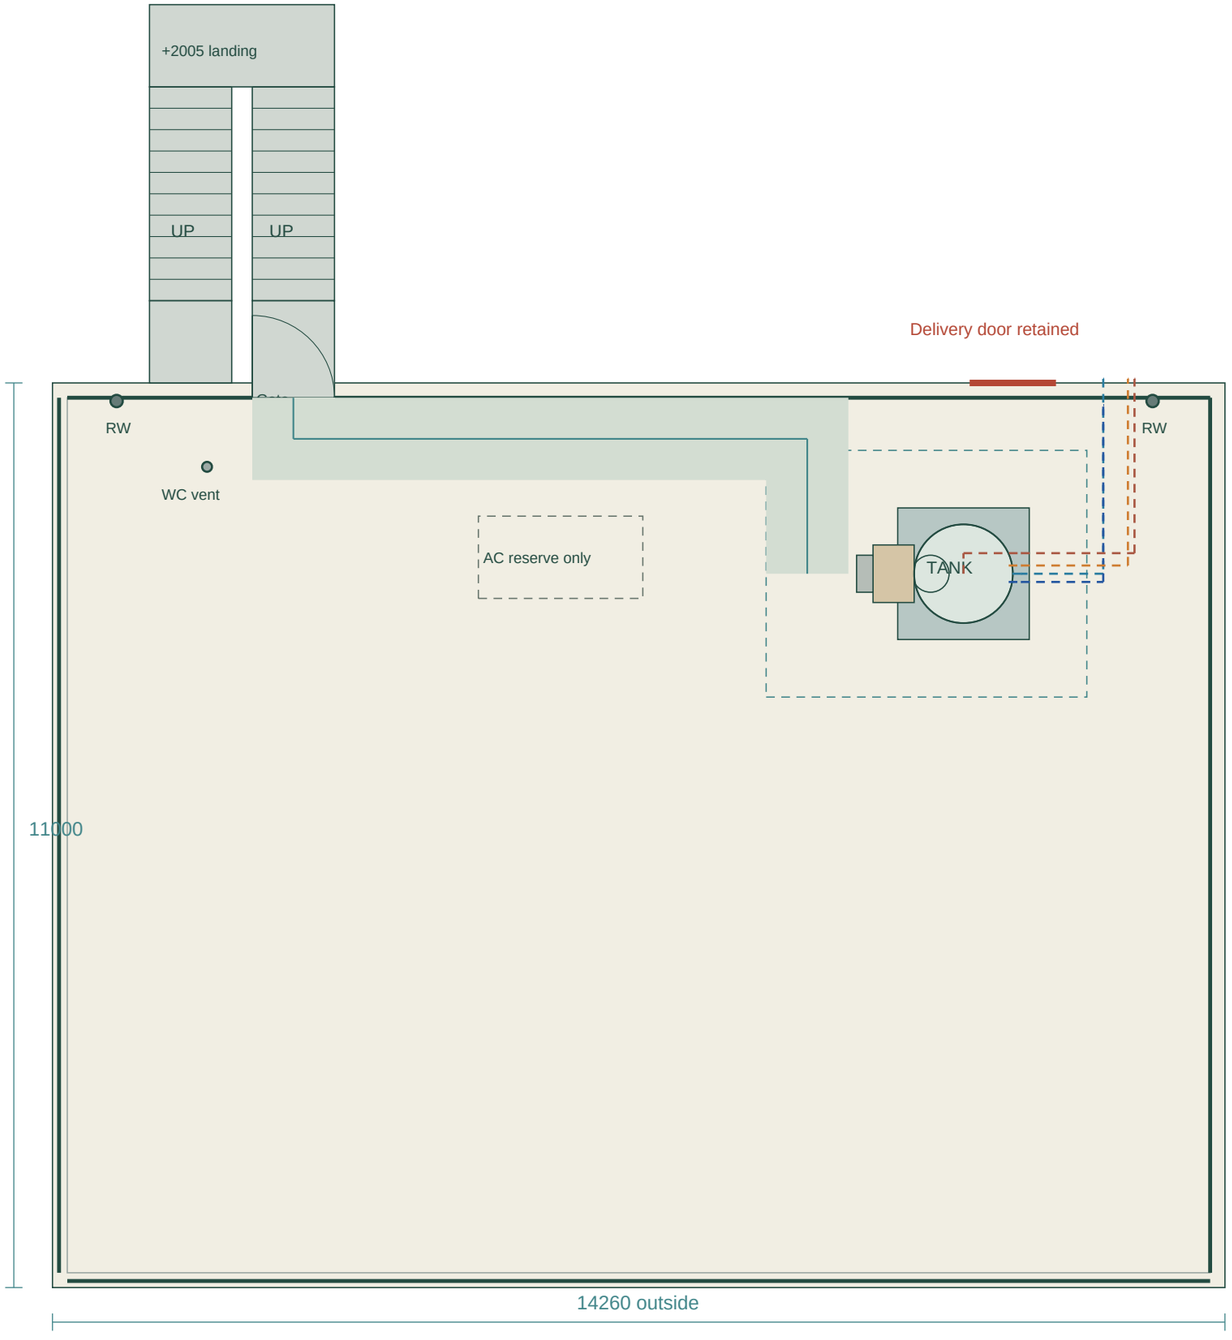

Tank: diameter1200 x body1200; level stand1600 x1600, raised350. Tank top +5560; vent +5760.

1000 mm service route from the roof gate, clear of tank support, inspection steps, WC vent and equipment reserve.

External stair: two 1000 mm clear flights, 22 equal rises, top +4010, midpoint +2005. Requires4600 mm rear-yard projection.

Roof drainage: indicative1:100 finish fall toward rear RW drains; separate emergency scupper.


Dashed coloured lines: concealed/plenum pipe routes, not pipe obstacles laid across the walking route.

No upstairs room, second-storey door or internal stair. The service stair stays outside.

AUDIT HOLD: rear-yard dimensions and actual town/exterior registration are not verified. Do not construct this stair in runtime until those dependencies are resolved.

Roof access / equal-rise stair and level tank stand

Unfolded stair section; use the plan for its U-turn / dimensions are proposal geometry, not code certification

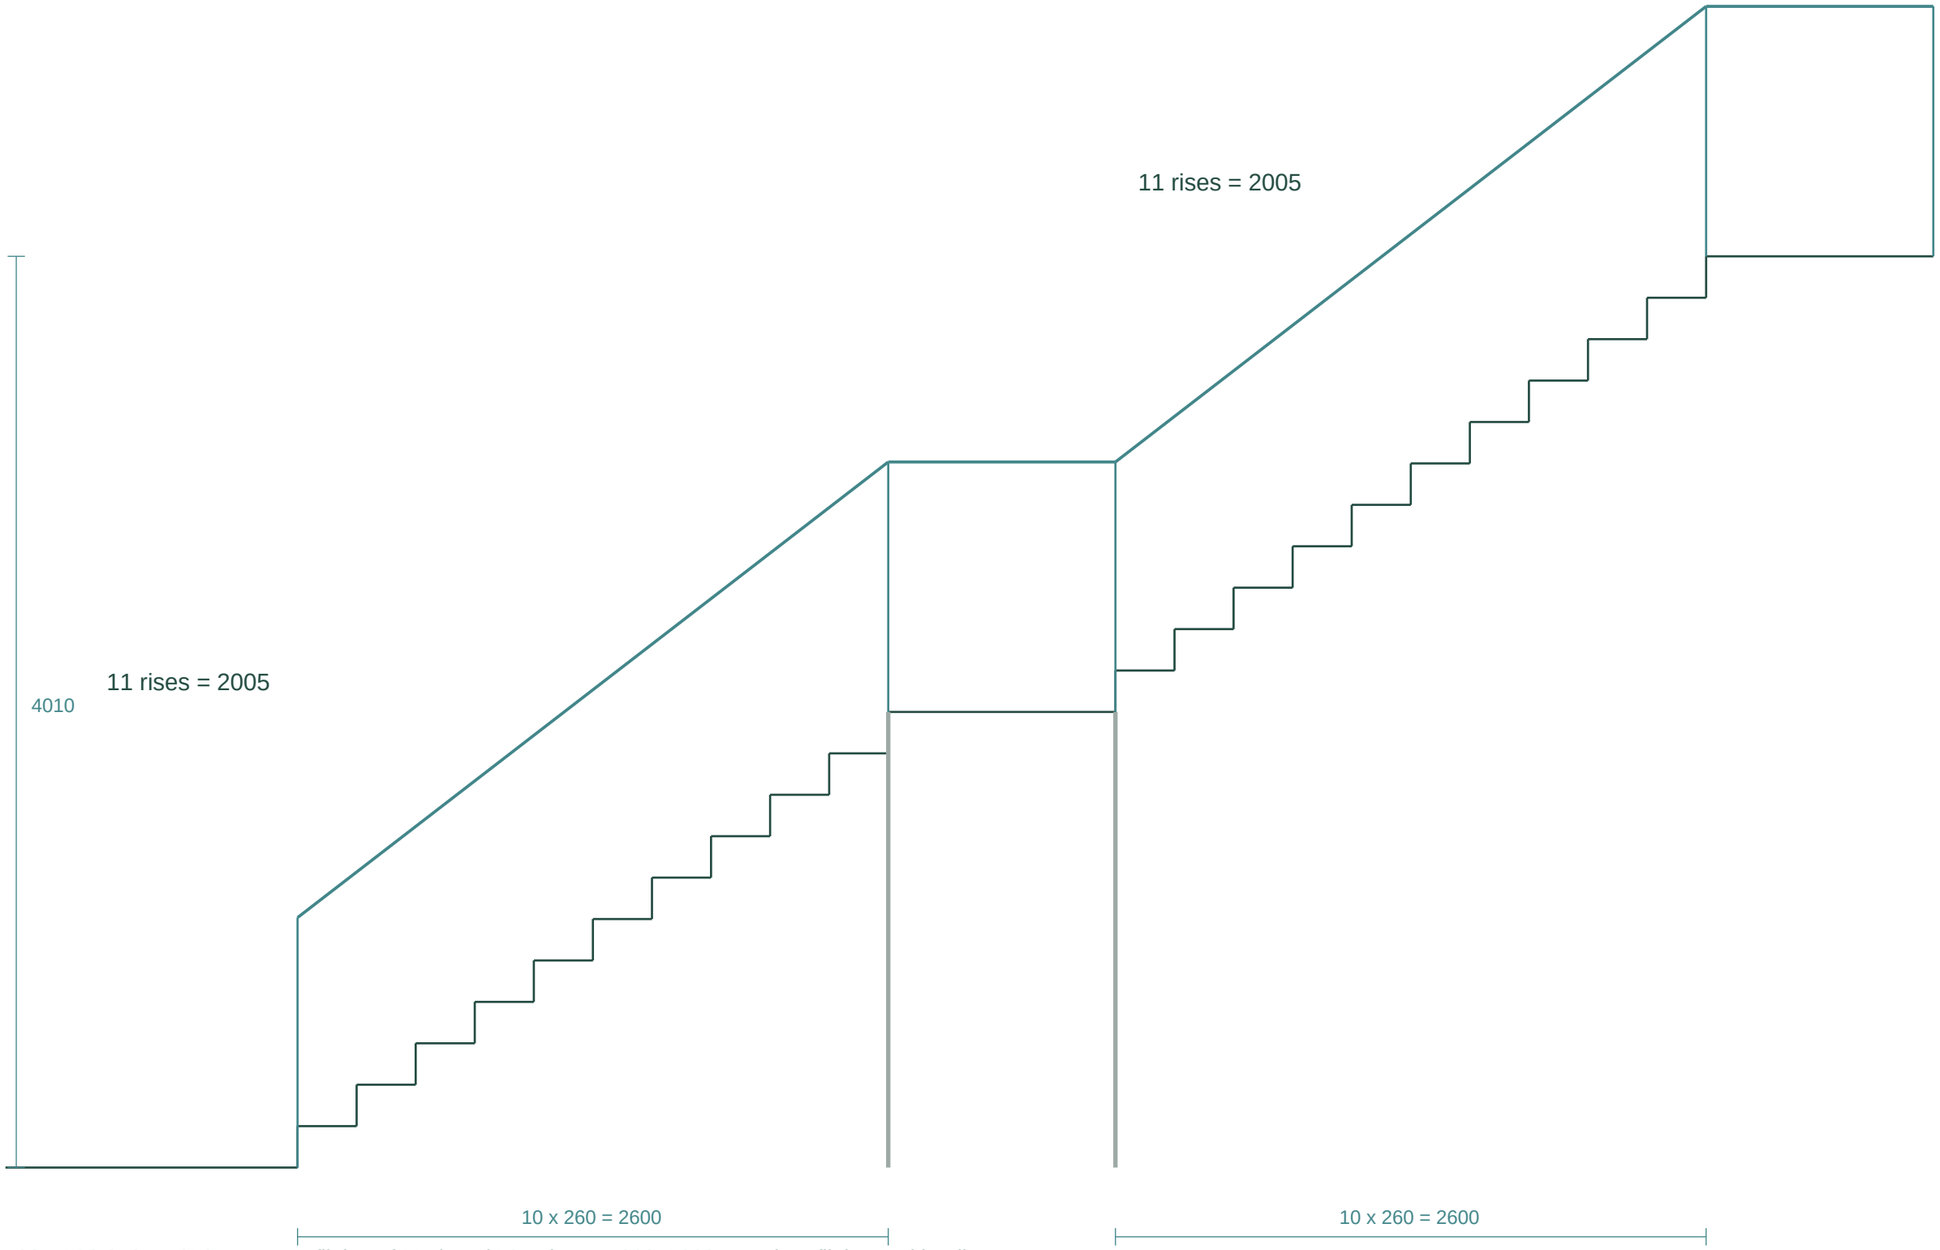

22 x 182.273 = 4010 mm. Two flights of 11 rises / 10 goings at 260; 1000 mm clear flights and landings.

Roof 4010 = wall 3860 + slab 150; ceiling 2800. Service void only. No upstairs room or internal stair.

Galvanised open steel treads/strings and 1100 guards. Gate opens toward external landing; U-turn is shown in plan.

350 mm tank stand clears the 4310 sleeve curb. Anchors, load path and 4600 mm rear-yard fit remain unverified.

Tank piping / fill, supply, overflow, drain and vent

Domestic-water visual coordination only / nominal pipe diameters are placeholders, not hydraulic sizing

CW-F DN25: rear meter/isolation at +600 -> concealed BOH plenum -> roof sleeve -> tank float inlet.


CW-S DN32: low tank outlet/isolation -> sleeve -> receiving manifold. Branches to staff washbasin, WC cistern and counter handwash.


OF DN50: screened overflow -> continuously descending dedicated route -> rear visible tundish/air gap.

DR DN25: low-point scour valve -> separate descending route -> visible air gap. No direct foul-waste connection.

VT DN50: downturned screened tank vent. Separate WC soil vent and DN75 rainwater downpipes.

Rear risers at X12600 /12900 /12980, outside north wall, clear of1050 delivery opening. All exposed lines get clamps; roof sleeves are flashed.

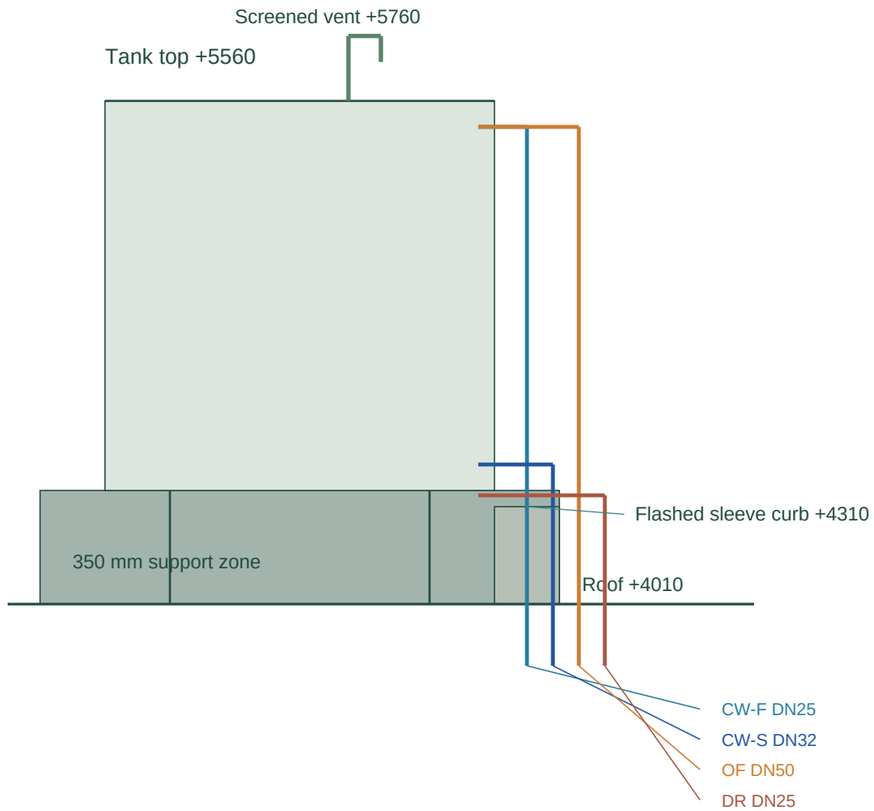


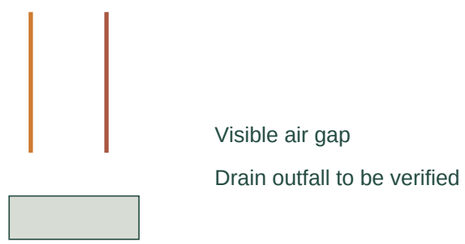

Audit: all fill/supply roof-level connections sit inside the protected tank/curb zone. The walking route has no horizontal pipe crossing. Pipe routes in the PDF section are schematic projections; exact3D coordinates are in design.json and the DXF PIPES_3D layer.


Exterior / street front and rear service elevation

Existing exterior shell and centred entrance retained / roof tank and rear services coordinated

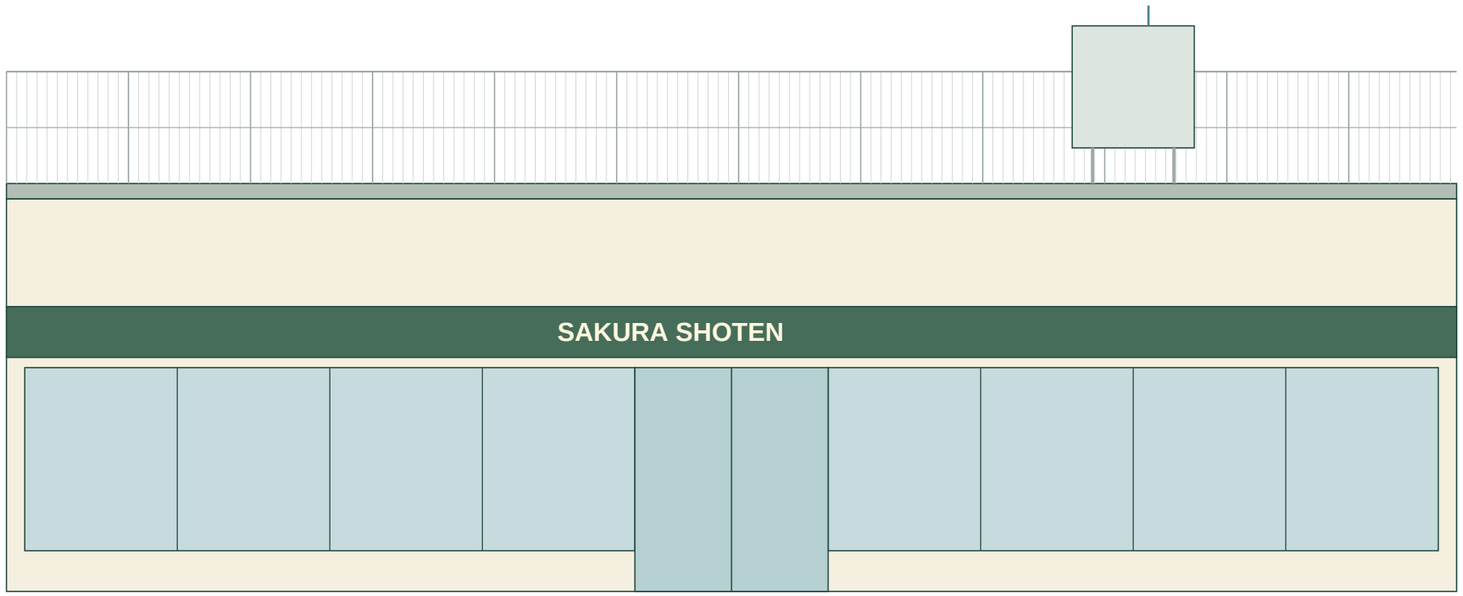

SOUTH / MAIN STREET

14260 outside

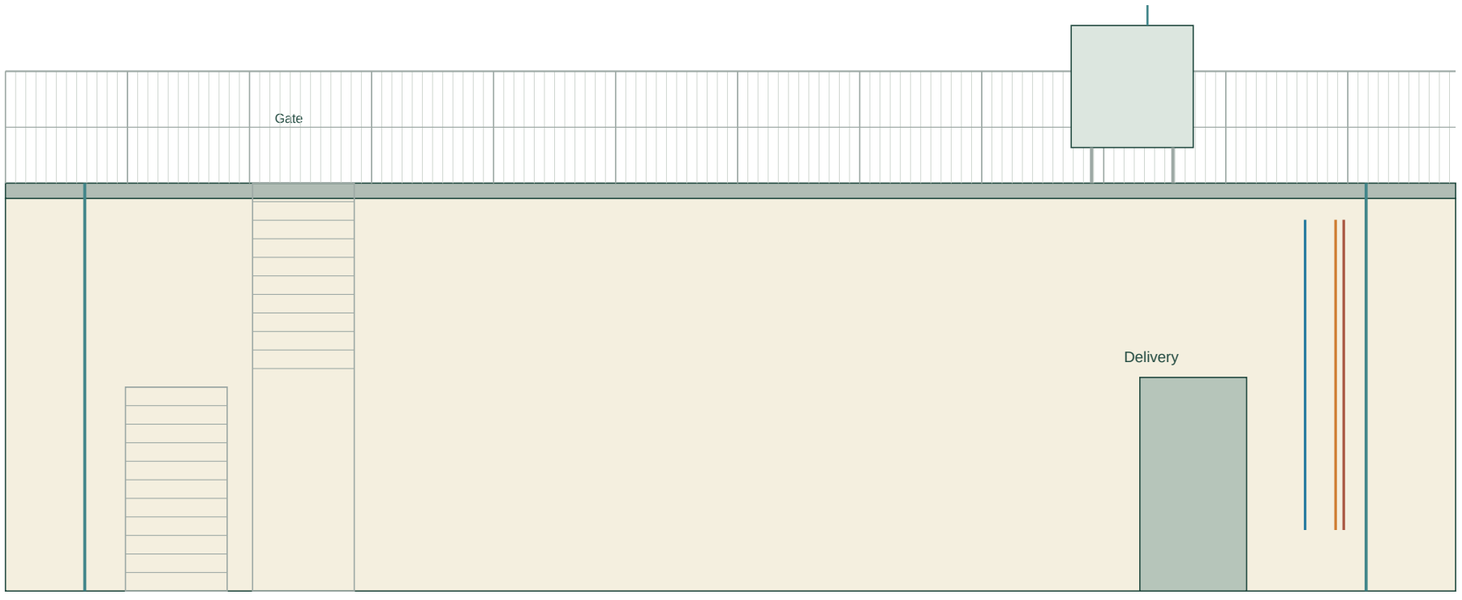

NORTH / DELIVERY AND ROOF ACCESS

14260 outside


Single storey: wall3860 / roof4010 / lightweight guards5110 / tank5560 / vent5760.

Rear stair shown in projection; its full4600 mm yard extension is on the roof plan.

Cream/timber identity and1900 entrance retained. Front mullions are proposed frame subdivision, not new openings.


Exterior / west and east side elevations

No new side doors, upstairs windows or internal stair / north at right in both coordination views

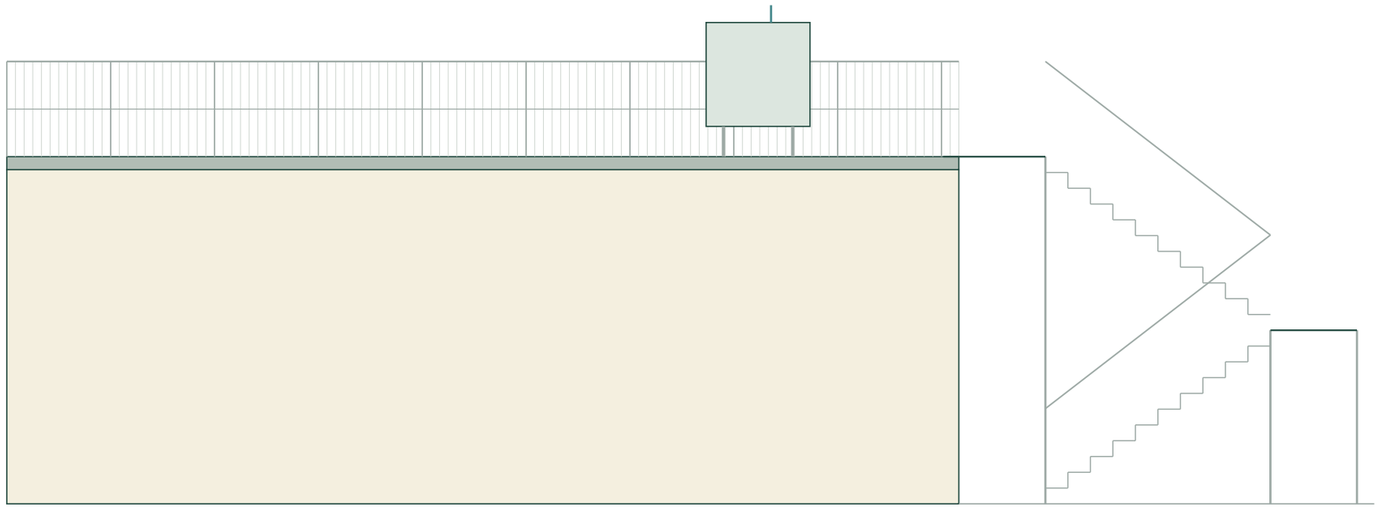

WEST / FRONT CORNER POSTER INSIDE

11000 outside

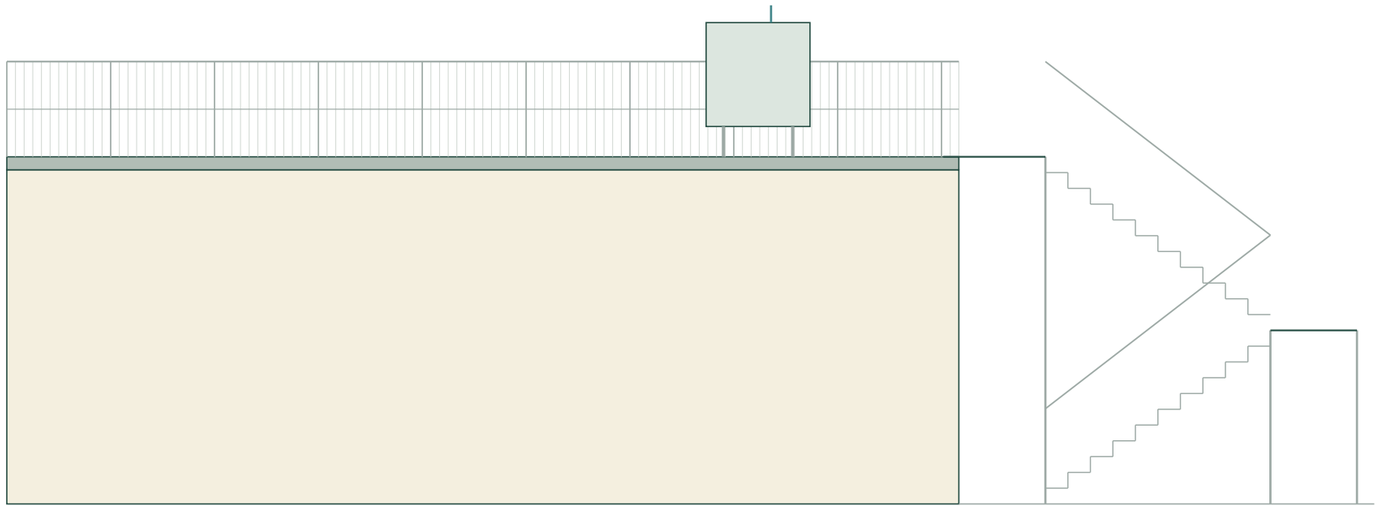

EAST / COUNTER SIDE

11000 outside

Solid side-wall mass retained.

Stair beyond the rear is shown in side projection; the actual U-plan determines both flights.

Tank, pipe upstands, guards, drainage and delivery fit must be registered to the town exterior before runtime construction.

AUDIT STATUS

Poster/notice overlap: zero.

22 equal stair rises: checked.

1000 service walk: clear.

DXF reopen: zero errors.

Open: site fit, anchors/load path, hydraulic sizing and actual exterior registration.

This package does not change the game runtime or establish a usable fire escape.